

PROPOSED DWELLING LOT 5051, 13 HOLBOURNE STREET, UPPER KEDRON, QLD, 4055

PROPOSED AREAS

GROUND FLOOR
LIVING - 195.90m²
GARAGE - 40.90m²
PORCH - 6.00m²
ALFRESCO - 17.50m²

TOTAL GF = 260.30m²

FIRST FLOOR
LIVING - 230.95m²
BALCONY - 10.75m²

TOTAL FF = 241.70m²

TOTAL AREA = 502.00m²


SITE INFORMATION

SITE AREA
MAX SITE COVERAGE = 50%
ACTUAL SITE COVERAGE
MAX HEIGHT

- 563m²
- 281.50m²
- 260.30m²
- 9.5m

DRAWING LIST

Sheet Number	Sheet Name
A_0000	COVER SHEET
A_0500	SITE PLAN
A_1100	GROUND FLOOR PLAN
A_1200	FIRST FLOOR PLAN
A_1300	ROOF PLAN
A_1400	GROUND FLOOR PLAN - DIMENSIONED
A_1500	FIRST FLOOR PLAN - DIMENSIONED
A_1600	GROUND FLOOR - SLAB PLAN
A_1700	GROUND FLOOR - PLUMBING PLAN
A_1800	FIRST FLOOR - PLUMBING PLAN
A_2000	EXTERNAL ELEVATIONS
A_2100	EXTERNAL ELEVATIONS
A_3000	SECTIONS
A_3001	SECTIONS
A_5000	WINDOW & DOOR SCHEDULE
A_6000	LANDSCAPE DESIGN

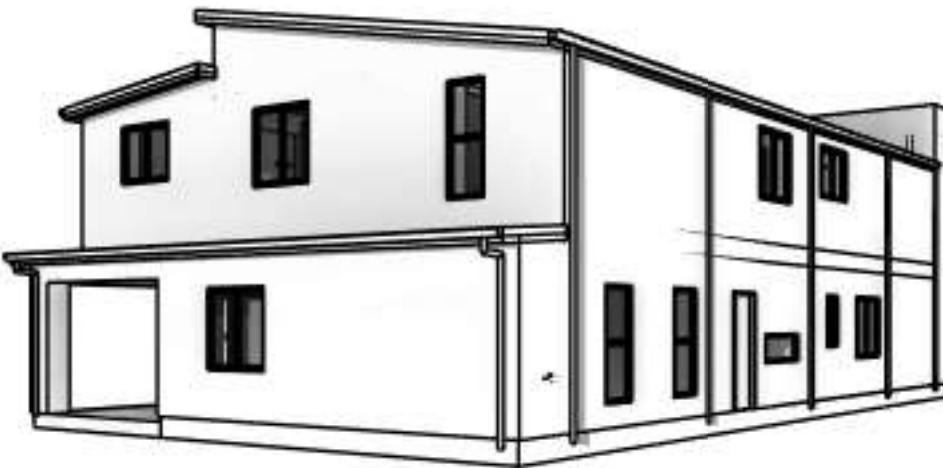

SIGMA BUILDING CERTIFICATION

APPROVED

Subject to Compliance with conditions endorsed.

Building Certifier - C.L. Fung

QBCC No. A15040934

B.A. No.: 25017

Date: 17/12/2025



ACN 669 609 536
QBCC 15405403

REFERENCE

NORTH

NOTES

1. Do not scale drawing. Written dimensions govern
2. All dimensions are in millimeters unless noted otherwise
3. All dimensions shall be verified on site before proceeding with the work. The Architect shall be notified in writing of any discrepancies.
4. This drawing must be read in conjunction with all relevant contracts, specifications and drawings

REV DESCRIPTION

- | | |
|---|----------------|
| A | CONCEPT DESIGN |
| B | CONCEPT DESIGN |
| C | CONCEPT DESIGN |
| D | CONCEPT DESIGN |
| E | CONCEPT DESIGN |
| F | CONCEPT DESIGN |
| G | FOR APPROVAL |

DATE

- | |
|------------|
| 12.07.2025 |
| 19.07.2025 |
| 25.07.2025 |
| 02.08.2025 |
| 16.08.2025 |
| 01.09.2025 |
| 15.10.2025 |

CLIENT

PROJECT

LOT 5051, 13 HOLBOURNE STREET, UPPER KEDRON, QLD, 4055

STATUS

FOR APPROVAL

DRAWING TITLE

COVER SHEET

REVIEWED

SR

APPROVED

LF

DRAWING NO.

A15040934

REV NO

G



SIGMA BUILDING CERTIFICATION

APPROVED


Subject to Compliance with conditions endorsed.

Building Certifier - C.L. Fung

QBCC No. A15040934


Date: 17/12/2025

B.A. No.: 25017

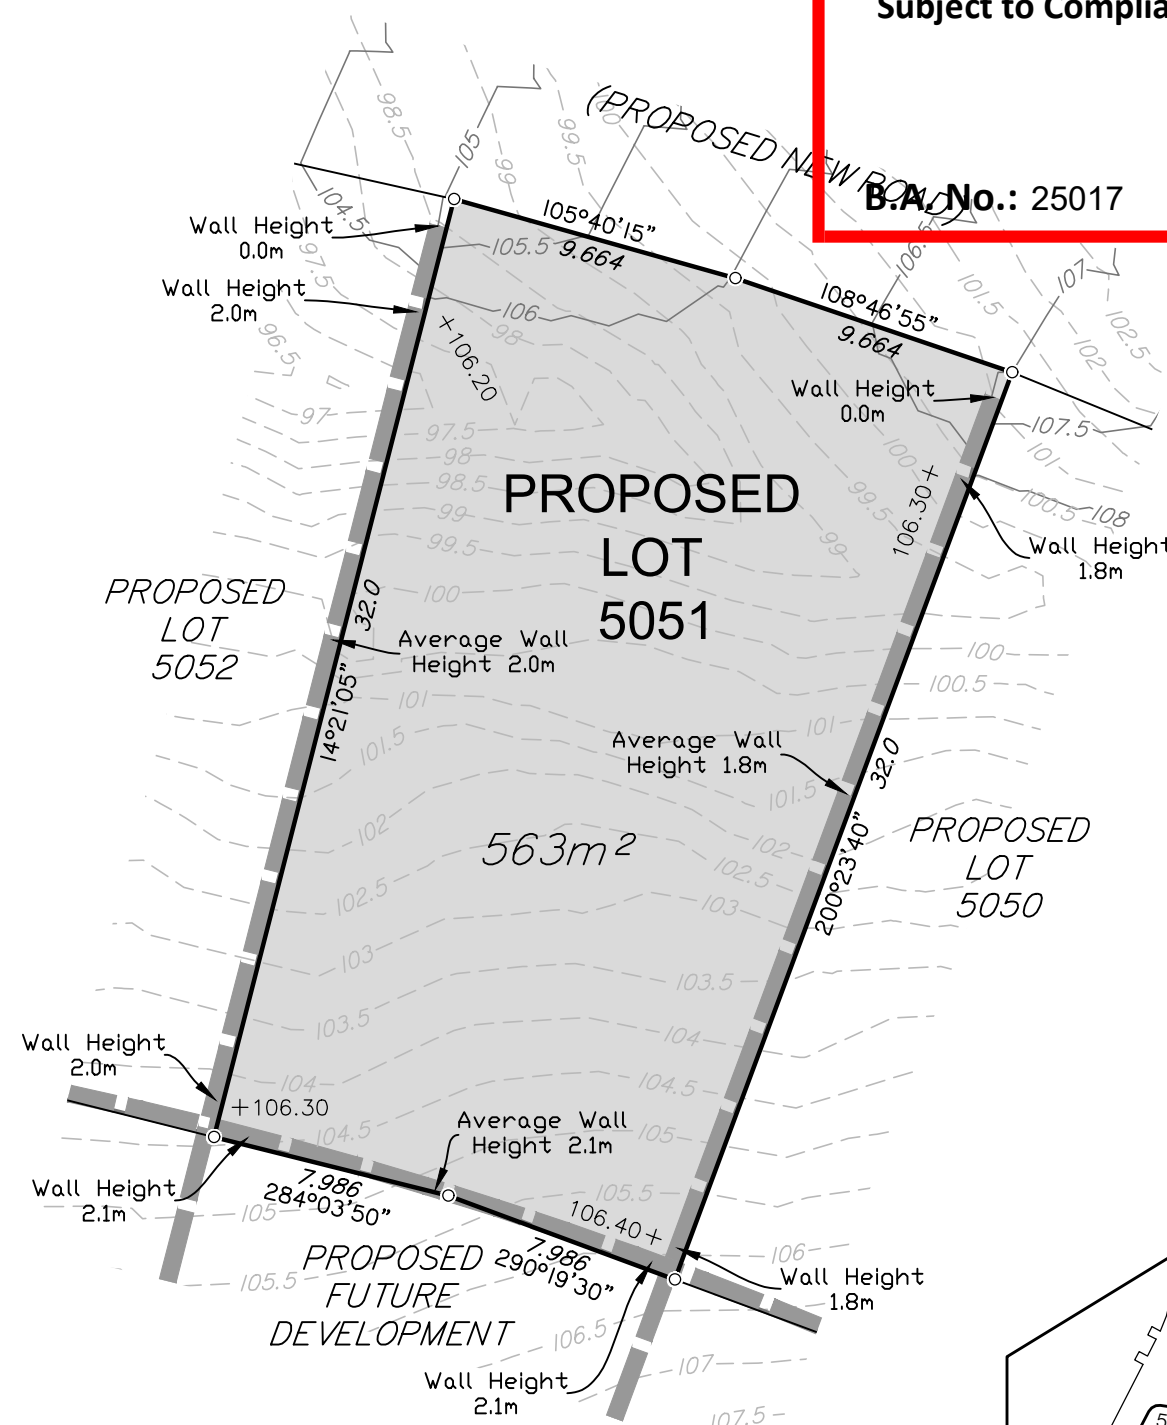

5 0 2 5 10m

SCALE 1:250

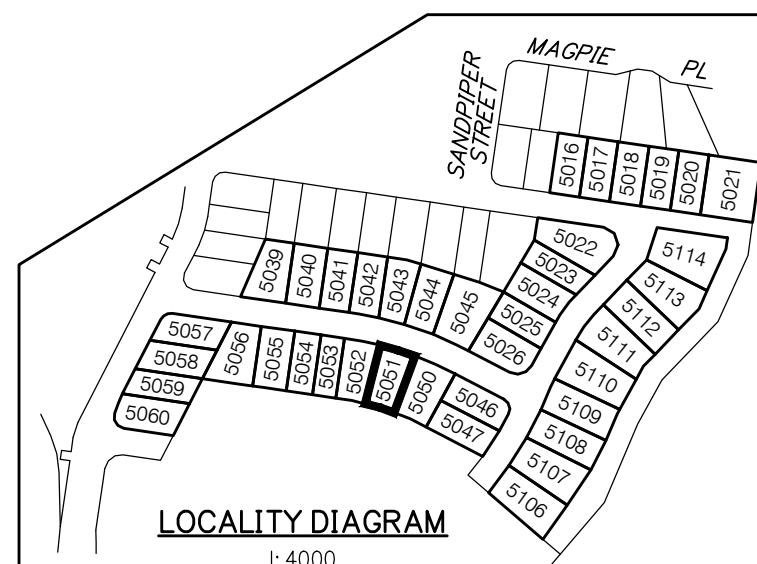

LOCALITY DIAGRAM

1: 4000

DISCLOSURE PLAN FOR PROPOSED LOT 5051

This plan shows:
Details of Proposed Lot 5051 on the Reconfiguration Plan from URBIS,
Drawing: ROL05.

A Reconfiguration of a lot application, being an application to
reconfigure Lot 3010 on SP303745 at Upper Kedron is subject to
Planning and Environment Court Appeal no. 969 of 2021
[BCC-CI.URI20320063].

This Disclosure Plan was prepared in accordance with the Land Sales
Act 1984 to enable the sale of proposed lots. **This plan should not be
used for design purposes as the details shown on this plan may vary
from final site conditions. Cedar Woods Properties Limited
recommends using As Constructed information for design purposes.**

Engineering details shown hereon were supplied by
COLLIERS on 1st May 2024.

Design surface contours based on AHD D — 63.5 —
datum at an interval of 0.5m, shown as:

Natural surface contours based on AHD D — 64.5 —
datum at an interval of 0.5m, shown as:

Retaining Walls are shown as: 
Retaining Wall linetype is not to scale and does not
represent final wall dimensions and materials.

Where applicable areas to be filled are shown as: 

The difference between the design surface contours and the
natural surface contours is indicative of the depth of the fill
(where fill is shown).

Maximum Fill Depth: 9.4m

Compaction of fill will be carried out in accordance with
Australian Standard AS 3798-2007, with Level I certification.

Project:

**ELLENDALE
UPPER KEDRON
STAGE 5B**

Client:



ellendale
UPPER KEDRON



Brisbane Office
Level 1
18 Little Cribb Street
Milton QLD 4064



PO Box 1399
Milton
QLD 4064



p: (07) 3842 1000
f: (07) 3842 1001
e: info@landpartners.com.au
w: www.landpartners.com.au

Items included in this section are in addition to standard Disclosure Plan requirements
(as defined in the Land Sales Act 1984)

Where applicable, Easements are shown as: 

Design pad level spot heights are shown as: +87.60

NOTE:

This additional information is indicative only and has been taken
from various sources and is a representation of the proposed
infrastructure. The actual location should be checked on site
after completion of construction.

The dimensions and locations of the Easements may vary and are
subject to final Council approval.

DRAWN	KDM	DATUM	AHD D
DATE	16/05/2024	LEVEL ORIGIN	PM60661 RL 120.695
CHECKED	AW	COMPUTER FILE	WC006686-05B-1-4
DATE	16/05/2024	SCALE (@ A3)	1:250
APPROVED	PJB	PLAN NUMBER	WC006686-05B-23-3
DATE	16/05/2024		

TOTAL GF = 260.30m²

SITE AREA
MAX SITE COVERAGE = 50%
ACTUAL SITE COVERAGE
MAX HEIGHT

LIVING - 230.95m²
BALCONY - 10.75m²

TOTAL FF = 241.70m²

TOTAL AREA = 502.00m²

- 563m²
- 281.50m²
- 260.30m²
- 9.5m

SIGMA BUILDING CERTIFICATION

APPROVED


Subject to Compliance with conditions endorsed.

Building Certifier - C.L. Fung

QBCC No. A15040934

B.A. No.: 25017

Date: 17/12/2025

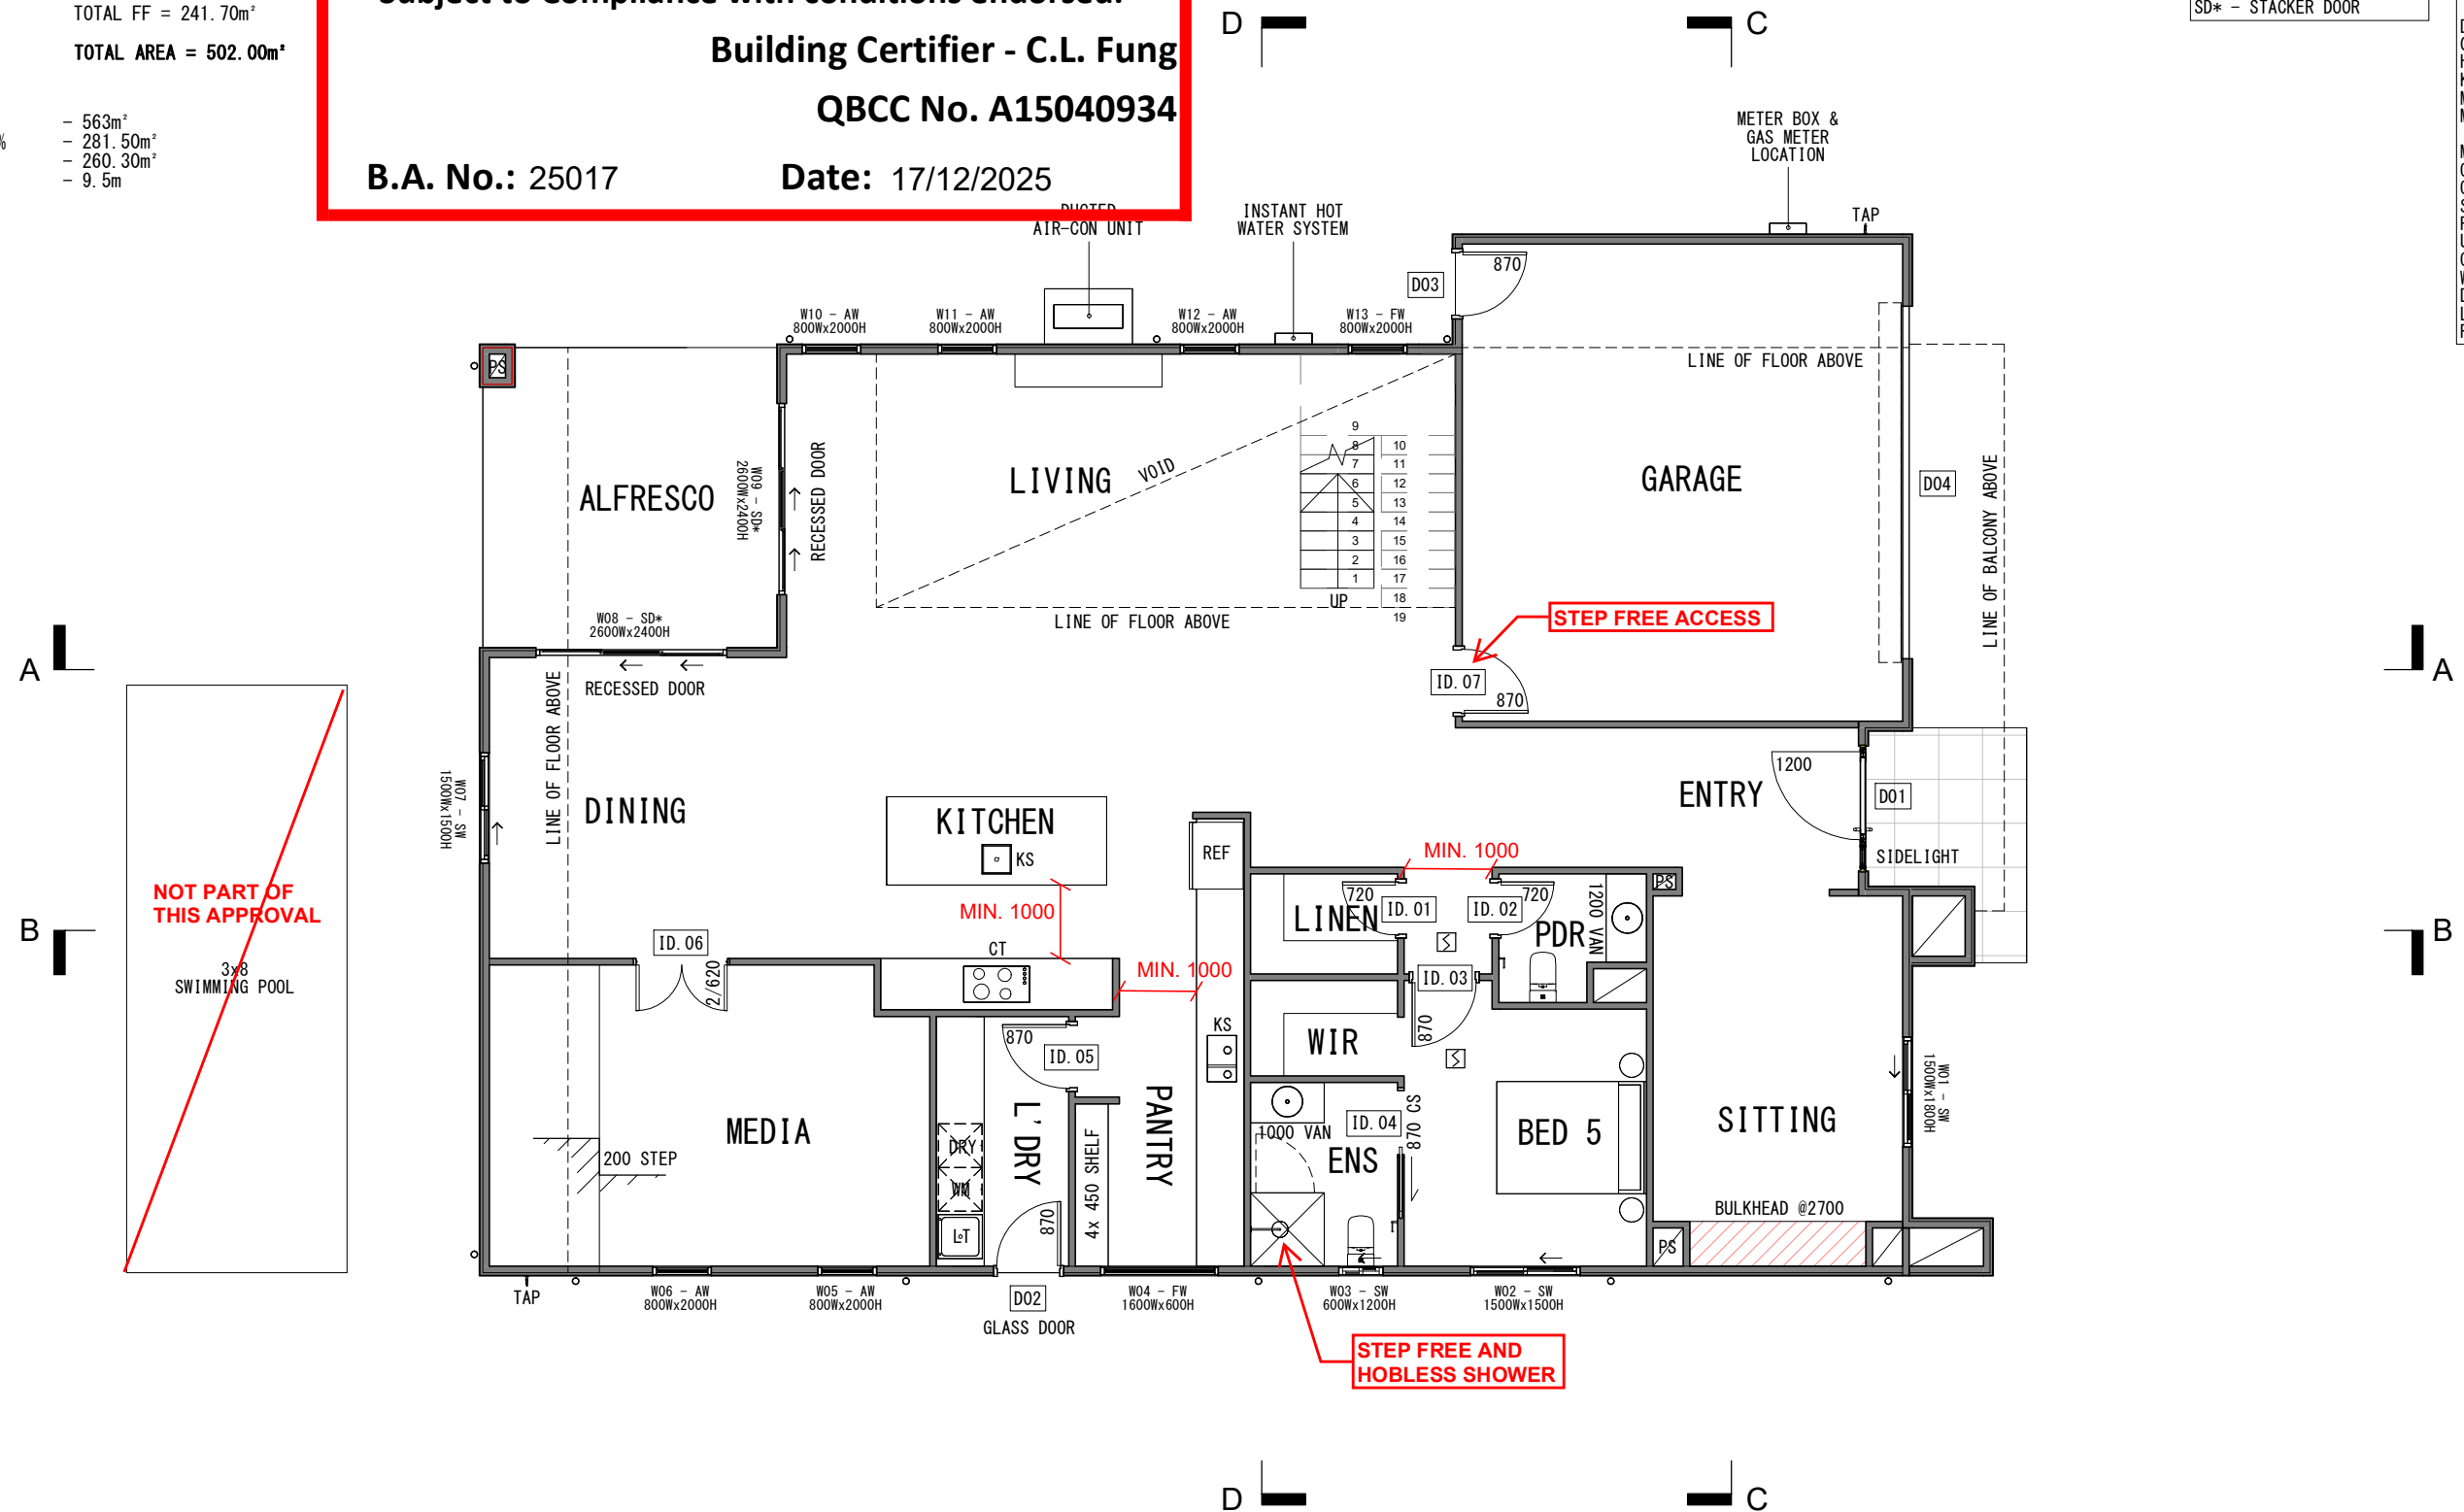

LEGEND - WINDOW AND DOOR

SW - SLIDING WINDOW
FW - FIXED WINDOW
AW - AWNING
DH - DOUBLE HUNG WINDOW
SD - SLIDING DOOR
SD* - STACKER DOOR


LEGEND - GENERAL

B/BAR	BREAKFAST BAR
BR	BROOM
CT	COOKTOP
DP	DOWNPIPE
DP/SP	DOWNPIPE WITH SPREADER
DW	DISHWASHER
GMB	GAS METERBOX
HWS	HOT WATER SYSTEM
KS	KITCHEN SINK
MB	METERBOX
MH	MANHOLE FOR CEILING ACCESS
MW	MICROWAVE
OBS	OBSCURE GLAZING
OHC	OVERHEAD CUPBOARD
SHW	SHOWER
RH	RANGEHOOD
UBO	UNDERBENCH OVEN
OT	OVEN TOWER
WM	WASHING MACHINE
DRY	DRYER
LT	LAUNDRY TUB
REF	REFRIGERATOR



ACN | 669 609 536
QBCC | 15405403

REFERENCE

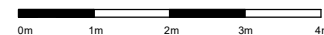

NORTH



NOTES

1. Do not scale drawing. Written dimensions govern
2. All dimensions are in millimeters unless noted otherwise
3. All dimensions shall be verified on site before proceeding with the work. The Architect shall be notified in writing of any discrepancies.
4. This drawing must be read in conjunction with all relevant contracts, specifications and drawings

REV	DESCRIPTION
-----	-------------

A	CONCEPT DESIGN
B	CONCEPT DESIGN
C	CONCEPT DESIGN
D	CONCEPT DESIGN
E	CONCEPT DESIGN
F	CONCEPT DESIGN
G	FOR APPROVAL

DATE _____

12.07.2025
19.07.2025
25.07.2025
02.08.2025
16.08.2025
01.09.2025
15.10.2025

| CLIENT

PROJECT
LOT 5051, 13 HOLBOURNE
STREET, UPPER KEDRON, QLD, 4055

STATUS
FOR APPROVAL

DRAWING TITLE
GROUND FLOOR PLAN

REVIEWED
SR

APPROVED
LH

DRAWING NO.
A 1100

A 1100

SCALE @ A3

1 : 100

PROJECT NO.
07-2025

07-2025

REV NO.

G

PROPOSED AREAS

GROUND FLOOR
LIVING - 195.90m²
GARAGE - 40.90m²
PORCH - 6.00m²
ALFRESCO - 17.50m²

TOTAL GF = 260.30m²

FIRST FLOOR
LIVING - 230.95m²
BALCONY - 10.75m²

TOTAL FF = 241.70m²


TOTAL AREA = 502.00m²

SITE INFORMATION

SITE AREA
MAX SITE COVERAGE = 50%
ACTUAL SITE COVERAGE
MAX HEIGHT

- 563m²
- 281.50m²
- 260.30m²
- 9.5m

LEGEND - GENERAL	
B/BAR	BREAKFAST BAR
BR	BROOM
CT	COOKTOP
DP	DOWNPIPE
DP/SP	DOWNPIPE WITH SPREADER
DW	DISHWASHER
GMB	GAS METERBOX
HWS	HOT WATER SYSTEM
KS	KITCHEN SINK
MB	METERBOX
MH	MANHOLE FOR CEILING ACCESS
MW	MICROWAVE
OBS	OBSCURE GLAZING
OHC	OVERHEAD CUPBOARD
SHW	SHOWER
RH	RANGEHOOD
UBO	UNDERBENCH OVEN
OT	OVEN TOWER
WM	WASHING MACHINE
DRY	DRYER
LT	LAUNDRY TUB
REF	REFRIGERATOR

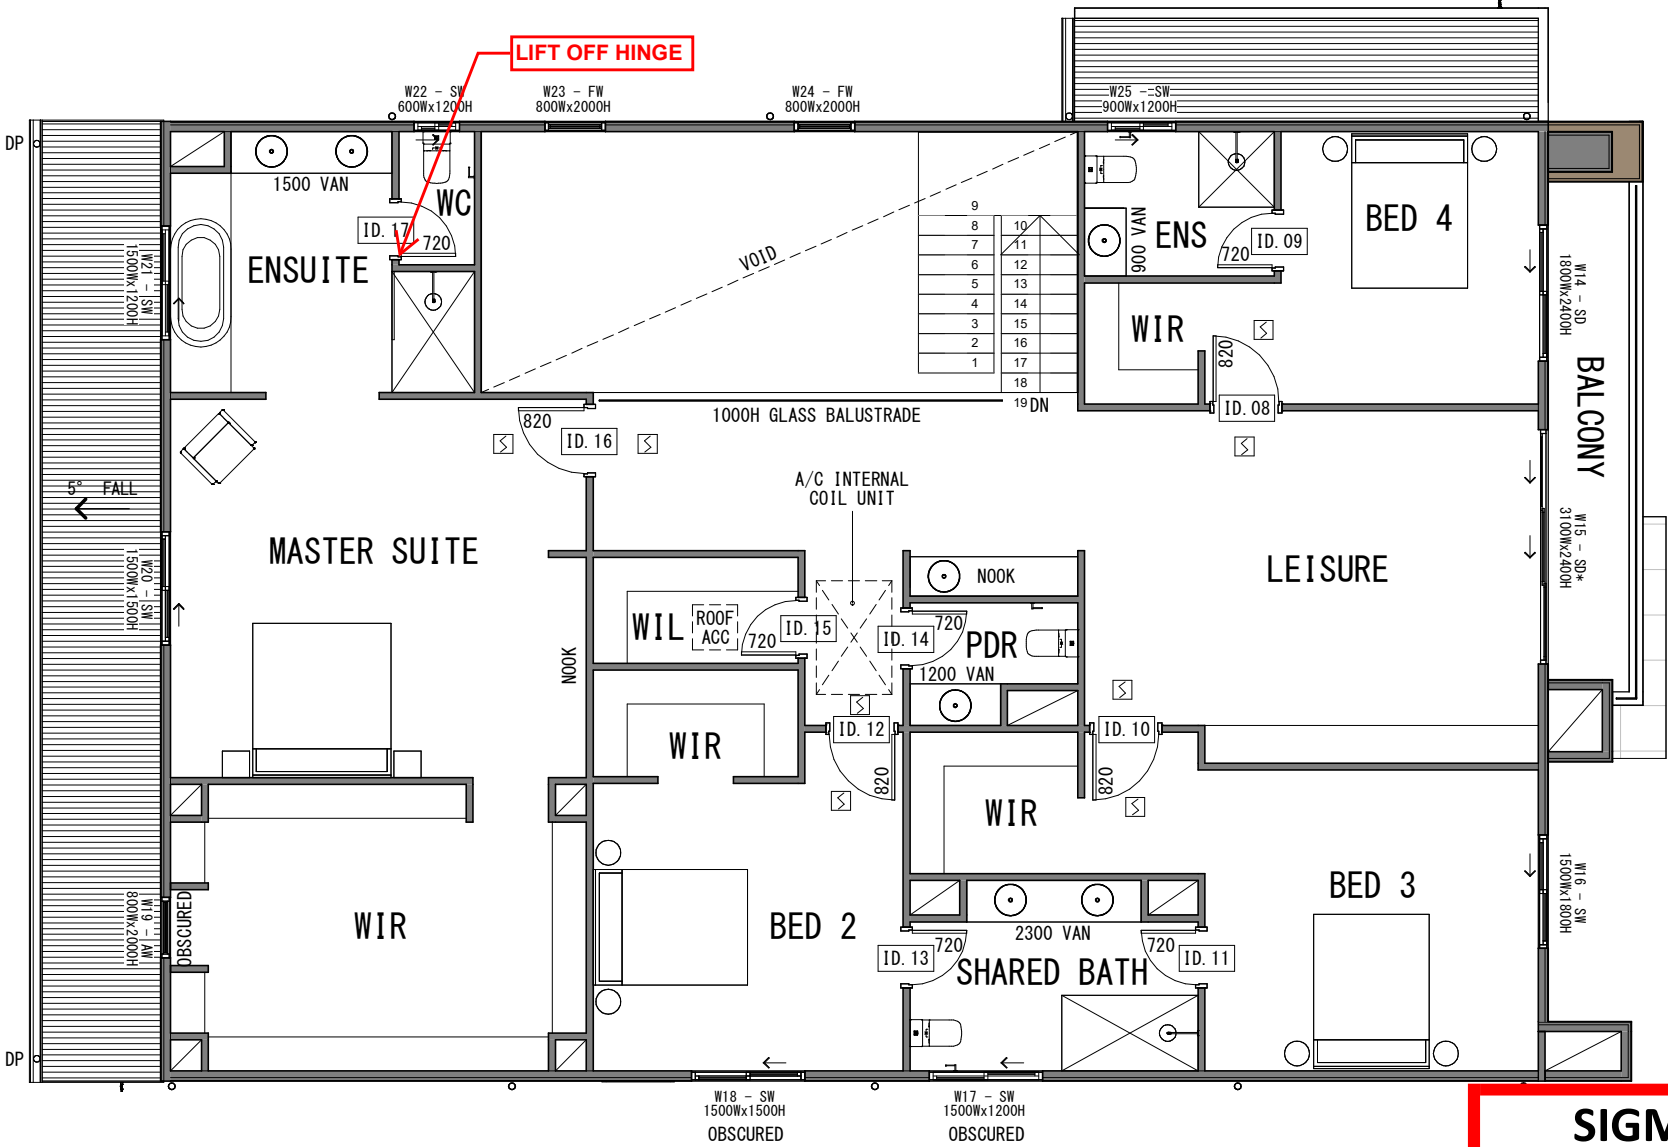

SIGMA BUILDING CERTIFICATION


APPROVED

Subject to Compliance with conditions endorsed.

Building Certifier - C.L. Fung
QBCC No. A15040934

B.A. No.: 25017

Date: 17/12/2025

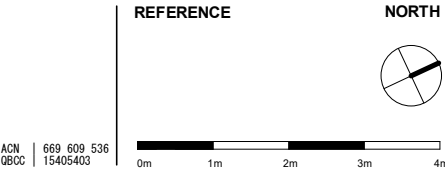

- NOTES
1. Do not scale drawing. Written dimensions govern
 2. All dimensions are in millimeters unless noted otherwise
 3. All dimensions shall be verified on site before proceeding with the work. The Architect shall be notified in writing of any discrepancies.
 4. This drawing must be read in conjunction with all relevant contracts, specifications and drawings

REV	DESCRIPTION
A	CONCEPT DESIGN
B	CONCEPT DESIGN
C	CONCEPT DESIGN
D	CONCEPT DESIGN
E	CONCEPT DESIGN
F	CONCEPT DESIGN
G	FOR APPROVAL

DATE	CLIENT
12.07.2025	
19.07.2025	
25.07.2025	
02.08.2025	
16.08.2025	
01.09.2025	
15.10.2025	

PROJECT
LOT 5051, 13 HOLBOURNE STREET, UPPER KEDRON, QLD, 4055

STATUS	DRAWING TITLE
FOR APPROVAL	FIRST FLOOR PLAN

REVIEWED	SCALE @ A3
SR	1 : 100
APPROVED	PROJECT NO.
LH	07-2025
DRAWING NO.	REV NO.
A_1200	G

SIGMA BUILDING CERTIFICATION

APPROVED


Subject to Compliance with conditions endorsed.

Building Certifier - C.L. Fung

QBCC No. A15040934

B.A. No.: 25017

Date: 17/12/2025

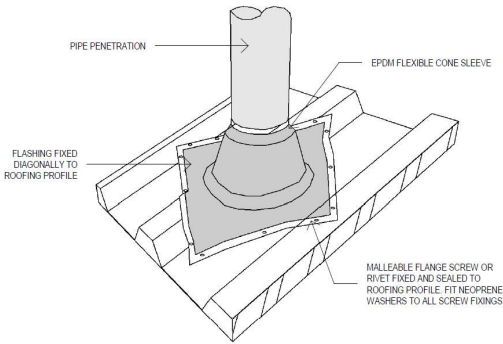


2 ROOF PIPE PENETRATION DETAIL

1:2

A

B

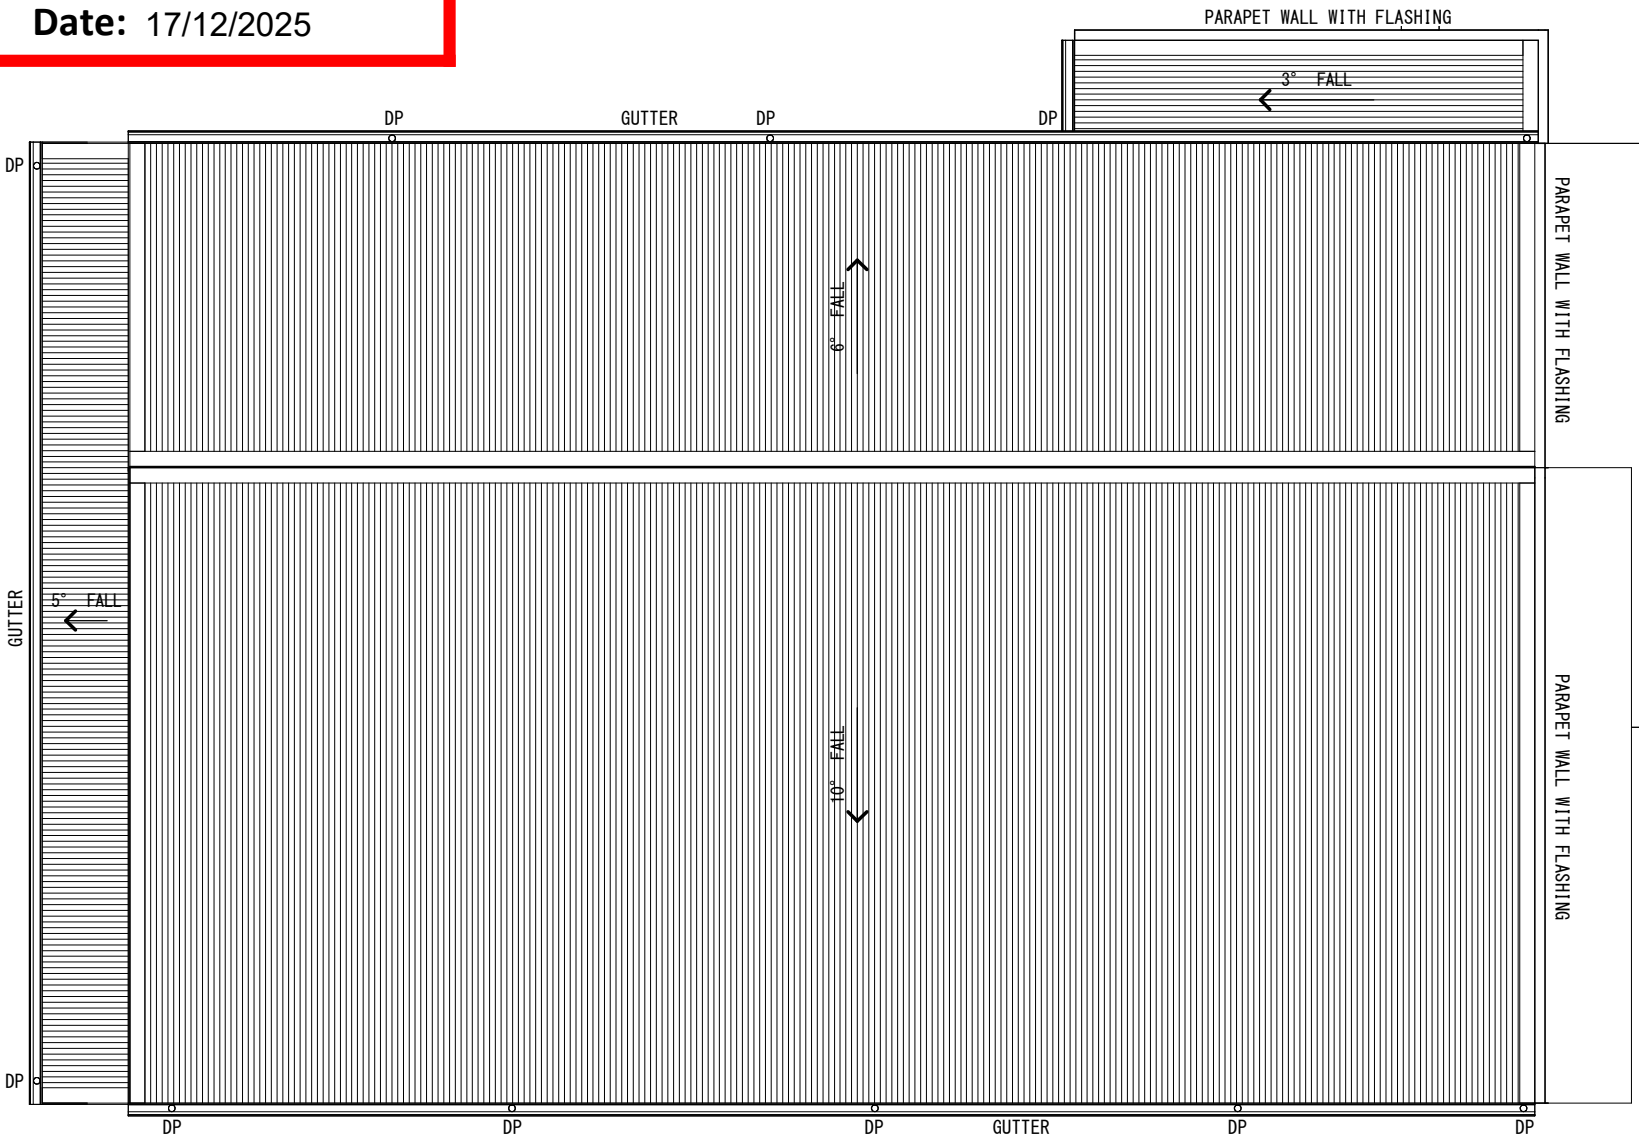

A

B

D

C

NOTE:

DOWNPIPES ARE TO SERVICE **12m** MAXIMUM GUTTER LENGTH & BE LOCATED AS CLOSE AS POSSIBLE TO VALLEY GUTTERS AND BE SELECTED IN ACCORDANCE WITH THE APPROPRIATE EAVES GUTTER SELECTION AS SHOWN IN (NCC VOL 2. TABLE 3.5.2.2)

GUTTERS, DOWNPIPES & FLASHINGS FABRICATED WITH METAL ARE TO MEET AS/NZ2179 REQUIREMENTS WHILE UPVC COMPONENTS ARE TO COMPLY WITH AS1273

ANY FLEXIBLE DUCTING THAT HAS A SOURCE FROM A FLAME HAZARD MUST MEET AS4254 HAZARD PROPERTIES

DOWNPIPES ARE TO BE PROTECTED FROM POTENTIAL MECHANICAL DAMAGE, BE INSTALLED NO LESS THAN **100mm** FROM ELECTRICAL CABLES & GAS PIPES & NO LESS THAN **50mm** FROM OTHER SERVICES (AS/NZS3500.3.2 S4.11)

CONNECT STORMWATER DRAINAGE TO LEGAL POINT OF DISCHARGE TO THE SATISFACTION OF THE RESPONSIBLE LOCAL AUTHORITY

CALCULATED ROOF CATCHMENTS & ROOFING TO BE INSTALLED AS PER AS/NZS3500.3

OVERFLOW MEASURERS IN ACCORDANCE WITH (NCC2016 VOL. 2 TABLE 3.5.2.4)

LOCATION AND SIZE OF DOWNPIPES TO BE CONFIRMED WITH PLUMBER ON SITE PRIOR TO INSTALLATION OF STORMWATER SERVICES.

LOCATION OF SOLAR HOT WATER PANELS & STANDARD SOLAR PANELS TO BE CONFIRMED BY CONTRACTOR. (IF APPLICABLE)



ACN 669 609 536
QBCC 15405403

REFERENCE

0m 1m 2m 3m 4m

NORTH



NOTES

1. Do not scale drawing. Written dimensions govern
2. All dimensions are in millimeters unless noted otherwise
3. All dimensions shall be verified on site before proceeding with the work. The Architect shall be notified in writing of any discrepancies.
4. This drawing must be read in conjunction with all relevant contracts, specifications and drawings

REV DESCRIPTION

- | | |
|---|----------------|
| A | CONCEPT DESIGN |
| B | CONCEPT DESIGN |
| C | CONCEPT DESIGN |
| D | CONCEPT DESIGN |
| E | CONCEPT DESIGN |
| F | CONCEPT DESIGN |
| G | FOR APPROVAL |

DATE

- | |
|------------|
| 12.07.2025 |
| 19.07.2025 |
| 25.07.2025 |
| 02.08.2025 |
| 16.08.2025 |
| 01.09.2025 |
| 15.10.2025 |

CLIENT

PROJECT
LOT 5051, 13 HOLBOURNE
STREET, UPPER KEDRON, QLD, 4055

STATUS
FOR APPROVAL

DRAWING TITLE
ROOF PLAN

REVIEWED
SR

APPROVED
LH

DRAWING NO.
A_1300

SCALE @ A3
1 : 100

PROJECT NO.
07-2025

REV NO.
G

SIGMA BUILDING CERTIFICATION

APPROVED


Subject to Compliance with conditions endorsed.

Building Certifier - C.L. Fung

QBCC No. A15040934

B.A. No.: 25017

Date: 17/12/2025

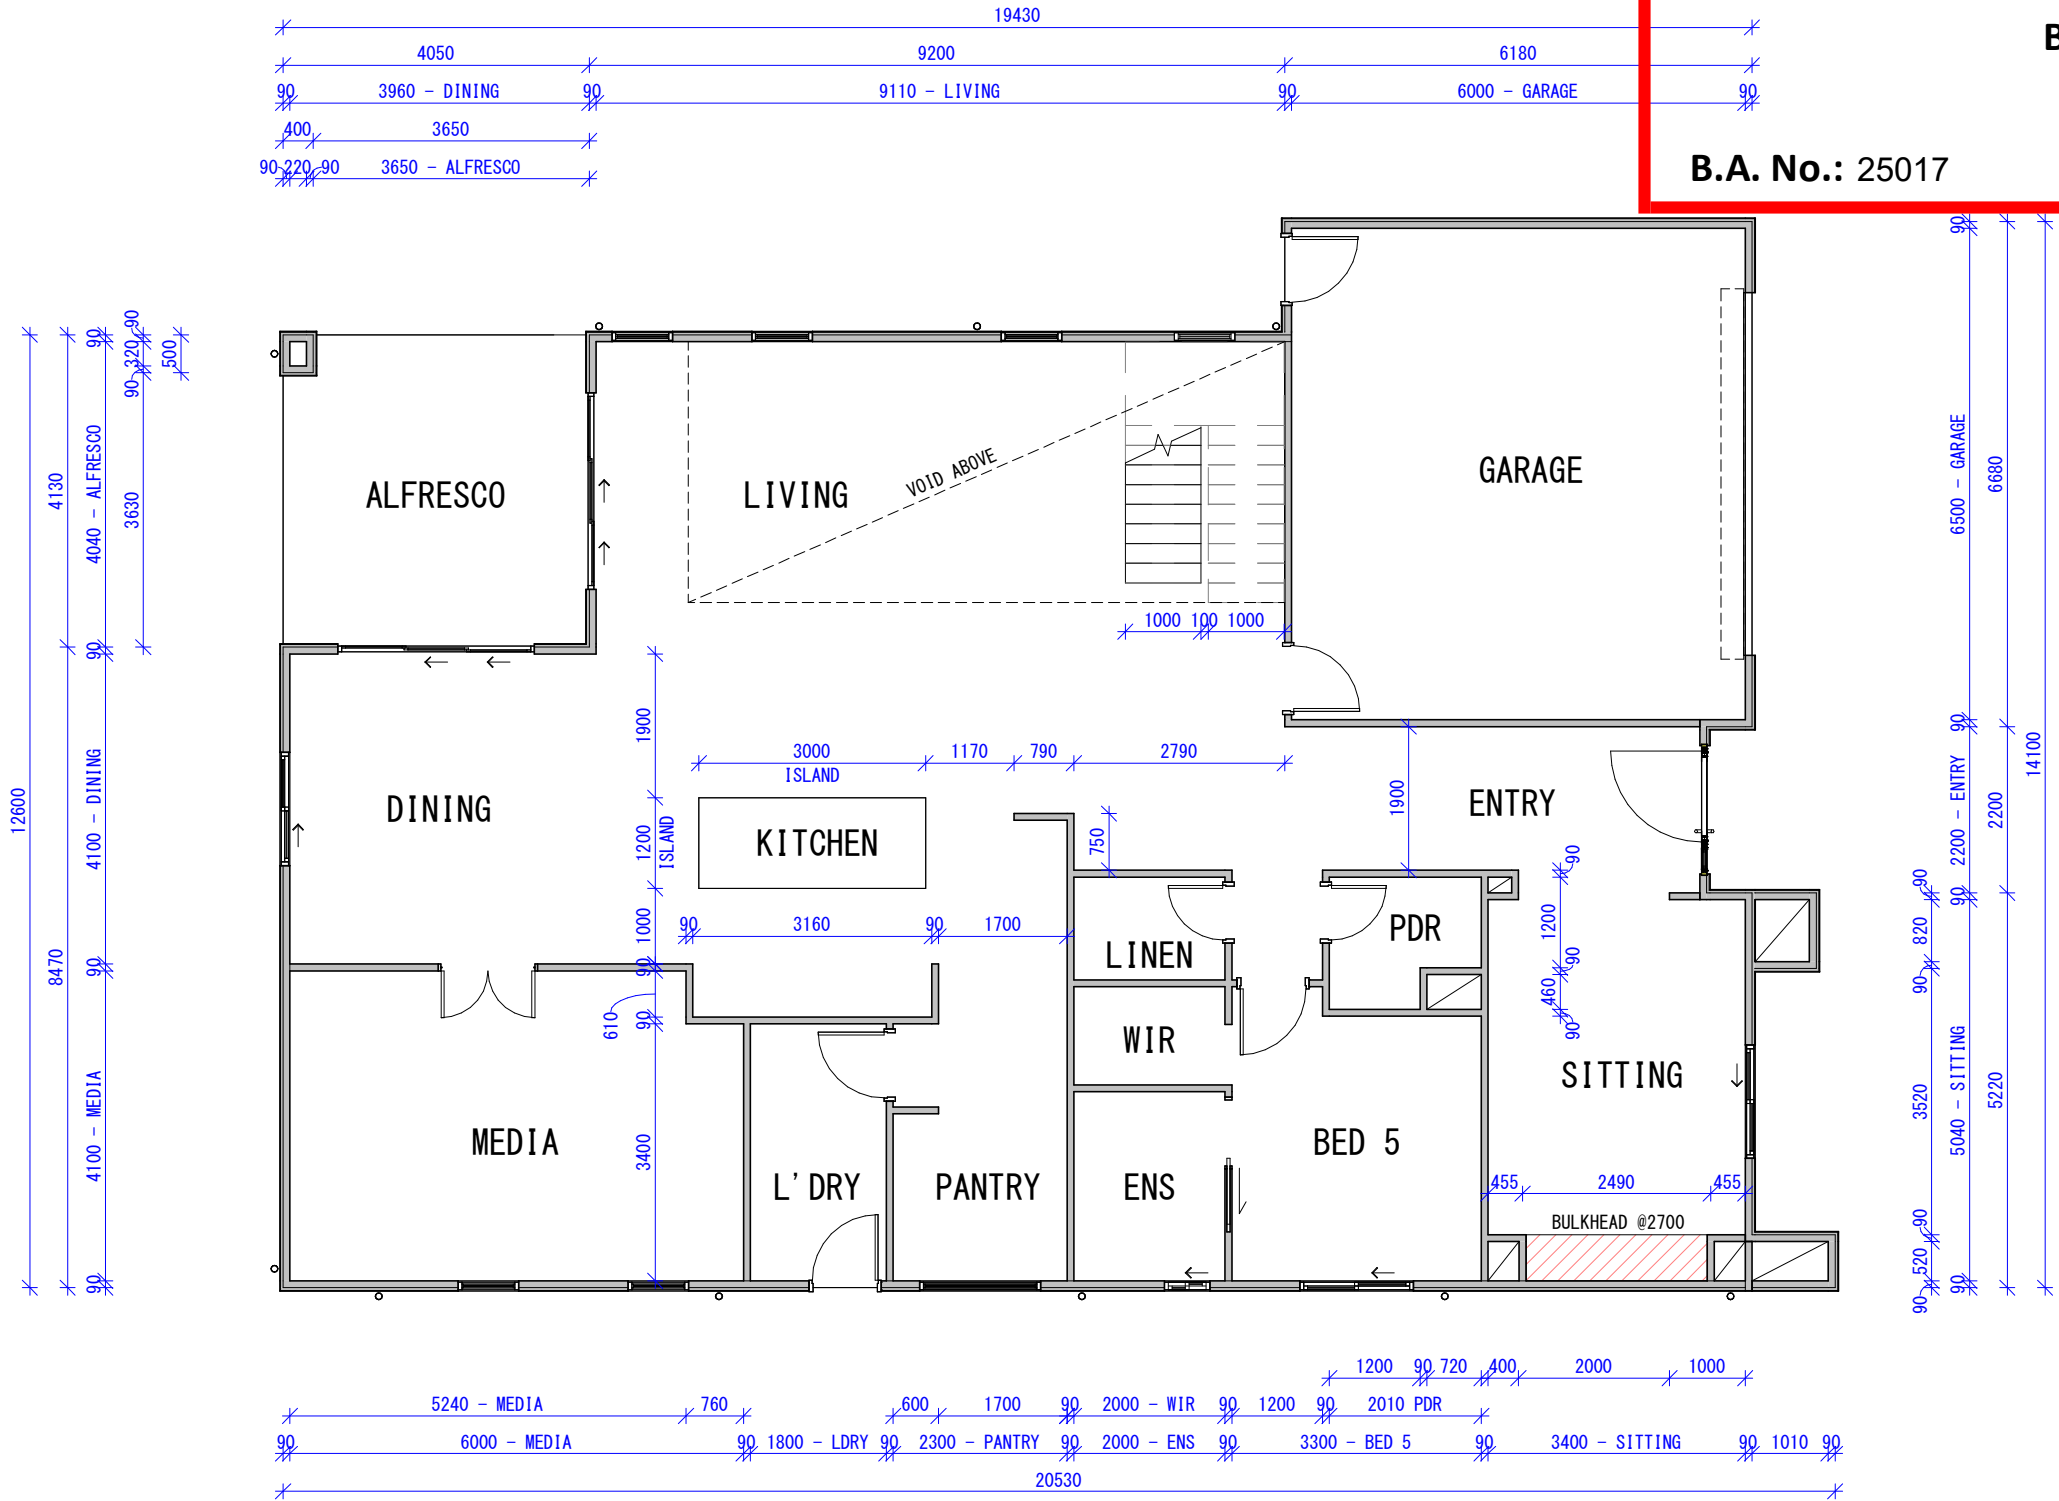

NOTE:
DIMENSIONS NOTED FRAME TO FRAME



ACN 669 609 536
QBCC 15405403

REFERENCE

0m 1m 2m 3m 4m

NORTH



NOTES

1. Do not scale drawing. Written dimensions govern
2. All dimensions are in millimeters unless noted otherwise
3. All dimensions shall be verified on site before proceeding with the work. The Architect shall be notified in writing of any discrepancies.
4. This drawing must be read in conjunction with all relevant contracts, specifications and drawings

REV DESCRIPTION

- | | |
|---|----------------|
| A | CONCEPT DESIGN |
| B | CONCEPT DESIGN |
| C | CONCEPT DESIGN |
| D | CONCEPT DESIGN |
| E | CONCEPT DESIGN |
| F | CONCEPT DESIGN |
| G | FOR APPROVAL |

DATE

- | |
|------------|
| 12.07.2025 |
| 19.07.2025 |
| 25.07.2025 |
| 02.08.2025 |
| 16.08.2025 |
| 01.09.2025 |
| 15.10.2025 |

CLIENT

PROJECT
LOT 5051, 13 HOLBOURNE
STREET, UPPER KEDRON, QLD, 4055

STATUS

FOR APPROVAL

DRAWING TITLE

GROUND FLOOR PLAN - DIMENSIONED

REVIEWED

SR

APPROVED

LH

DRAWING NO.

A_1400

SCALE @ A3

1 : 100

PROJECT NO.

07-2025

REV NO.

G




SIGMA BUILDING CERTIFICATION
APPROVED

Subject to Compliance with conditions endorsed.

Building Certifier - C.L. Fung
QBCC No. A15040934

B.A. No.: 25017

Date: 17/12/2025

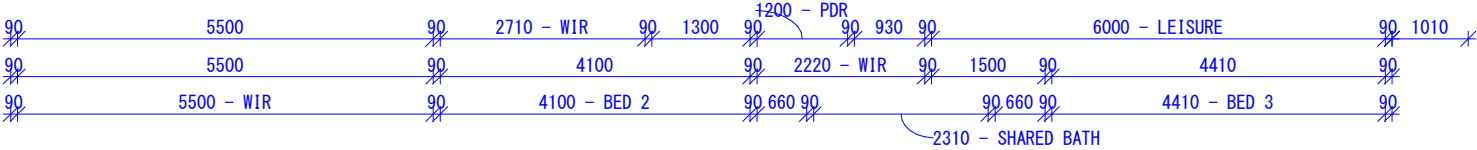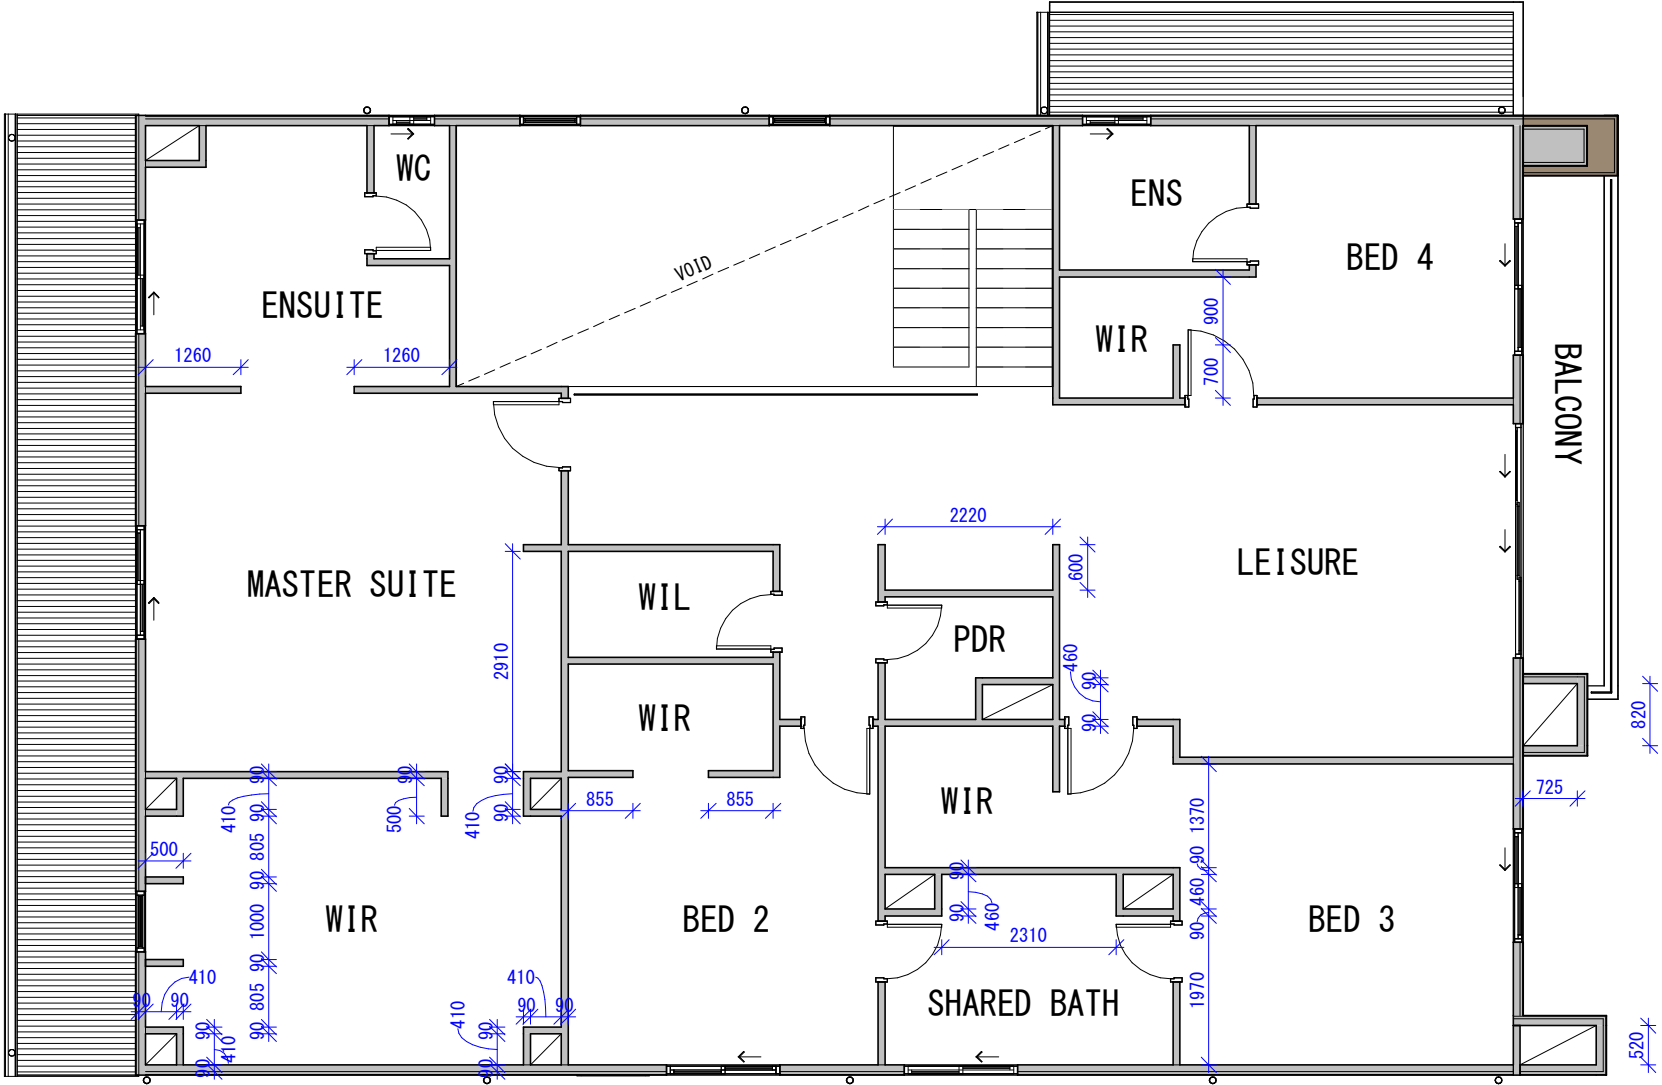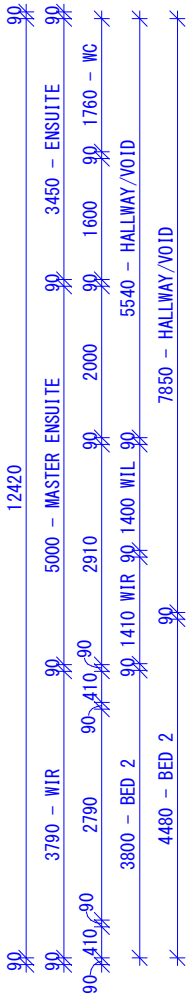


NOTE:
DIMENSIONS NOTED FRAME TO FRAME



ACN | 669 609 536
QBCC | 15405403

REFERENCE

 

NORTH



NOTES

1. Do not scale drawing. Written dimensions govern
2. All dimensions are in millimeters unless noted otherwise
3. All dimensions shall be verified on site before proceeding with the work. The Architect shall be notified in writing of any discrepancies.
4. This drawing must be read in conjunction with all relevant contracts, specifications and drawings

REV DESCRIPTION

- | | |
|---|----------------|
| A | CONCEPT DESIGN |
| B | CONCEPT DESIGN |
| C | CONCEPT DESIGN |
| D | CONCEPT DESIGN |
| E | CONCEPT DESIGN |
| F | CONCEPT DESIGN |
| G | FOR APPROVAL |

DATE

- | |
|------------|
| 12.07.2025 |
| 19.07.2025 |
| 25.07.2025 |
| 02.08.2025 |
| 16.08.2025 |
| 01.09.2025 |
| 15.10.2025 |

CLIENT

PROJECT
LOT 5051, 13 HOLBOURNE
STREET, UPPER KEDRON, QLD, 4055

STATUS
FOR APPROVAL

DRAWING TITLE
FIRST FLOOR PLAN - DIMENSIONED

REVIEWED
SR

APPROVED
LH

DRAWING NO.
A_1500

SCALE @ A3
1 : 100

PROJECT NO.
07-2025

REV NO.
G

SIGMA BUILDING CERTIFICATION

APPROVED


Subject to Compliance with conditions endorsed.

Building Certifier - C.L. Fung

QBCC No. A15040934

B.A. No.: 25017

Date: 17/12/2025

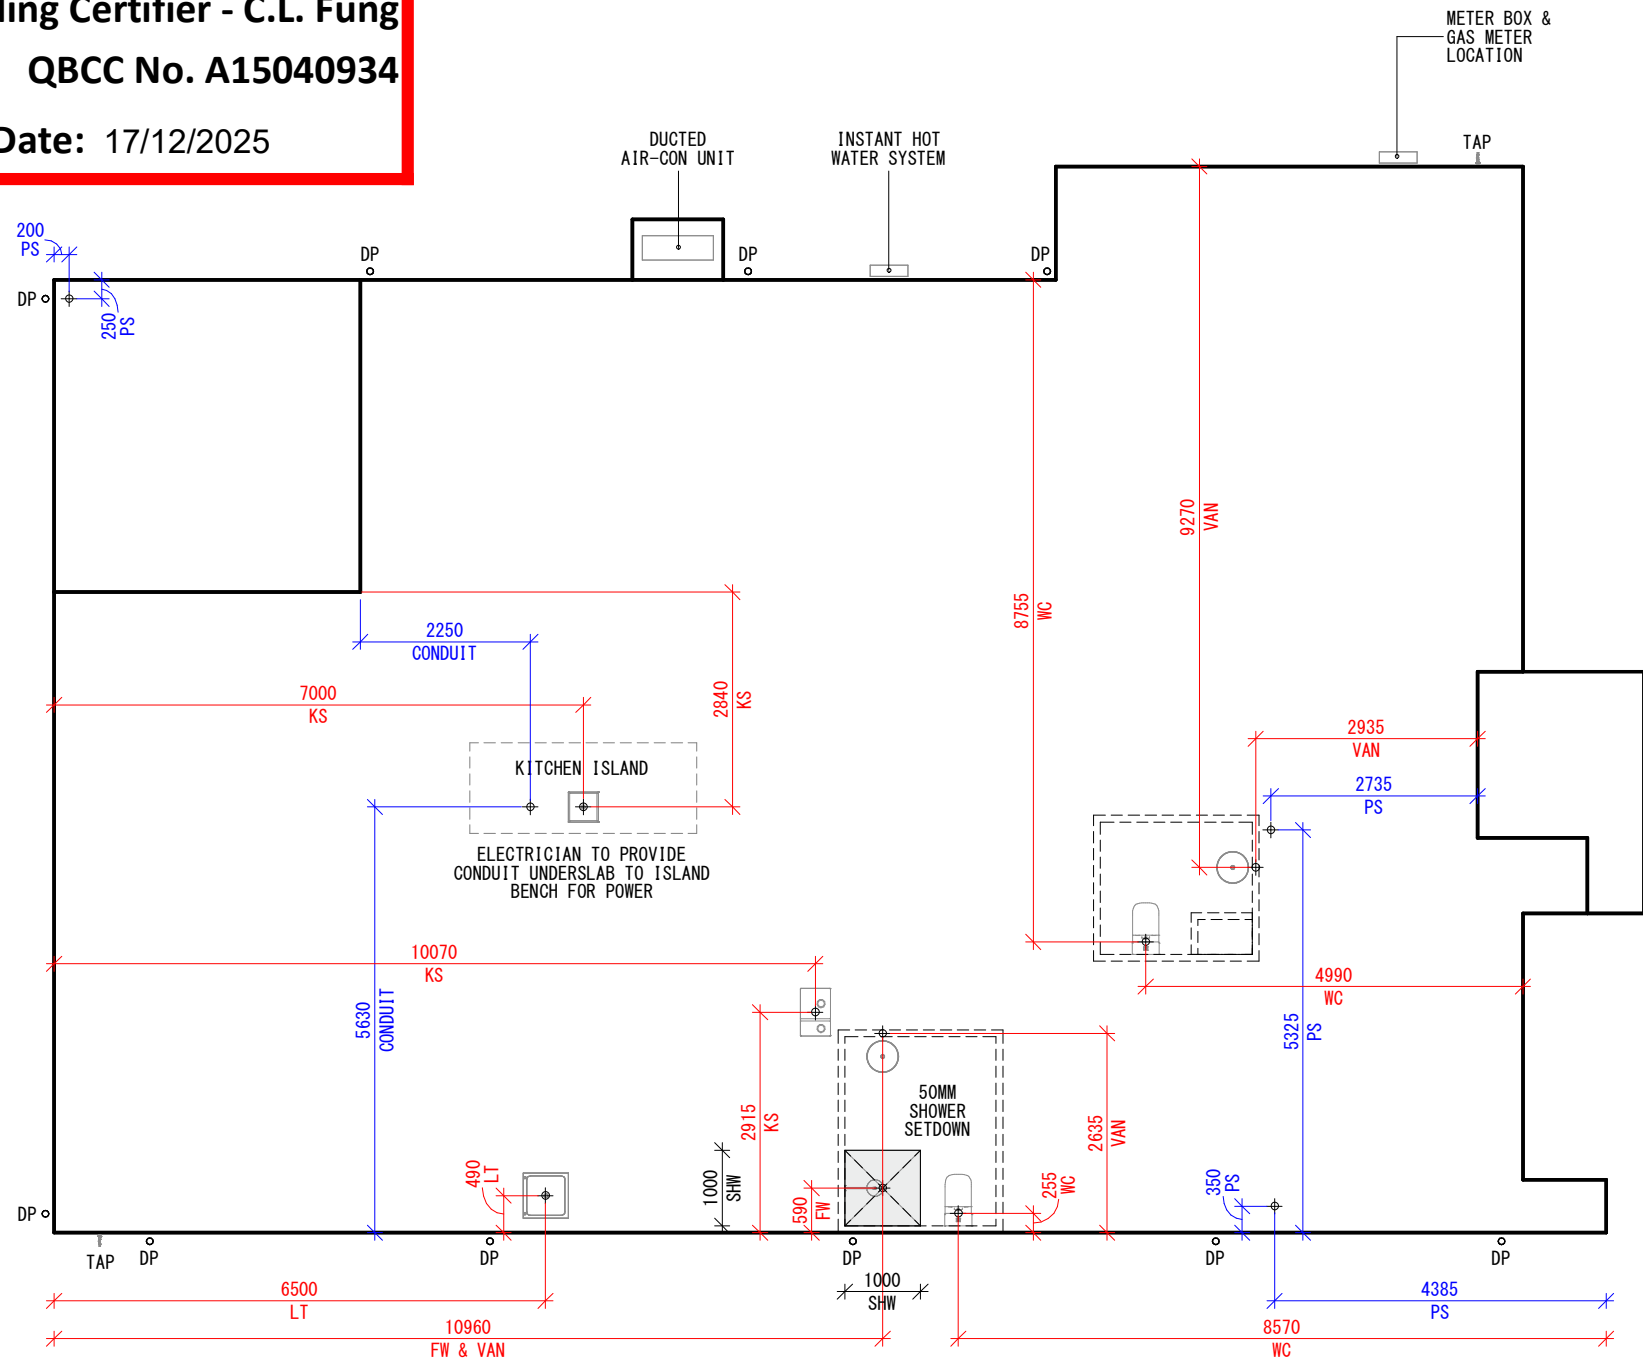


NOTE:
ALL PENETRATION DIMENSIONS ARE TAKEN FROM THE SLAB EDGE TO CL OF PENETRATION

PLUMBING LEGEND	
DP	DOWNPIPE
SHW	SHOWER
WC	TOILET
LT	LAUNDRY TUB
KS	KITCHEN SINK
FW	FLOOR WASTE
FWG	FLOOR WASTE GULLY
PS	PLUMBING STACK
VAN	VANITY
TAP	GARDEN TAP



ACN 669 609 536
QBCC 15405403

REFERENCE

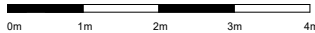

NORTH



NOTES

1. Do not scale drawing. Written dimensions govern
2. All dimensions are in millimeters unless noted otherwise
3. All dimensions shall be verified on site before proceeding with the work. The Architect shall be notified in writing of any discrepancies.
4. This drawing must be read in conjunction with all relevant contracts, specifications and drawings

REV DESCRIPTION

A	CONCEPT DESIGN
B	CONCEPT DESIGN
C	CONCEPT DESIGN
D	CONCEPT DESIGN
E	CONCEPT DESIGN
F	CONCEPT DESIGN
G	FOR APPROVAL

DATE

12.07.2025
19.07.2025
25.07.2025
02.08.2025
16.08.2025
01.09.2025
15.10.2025

CLIENT

PROJECT
LOT 5051, 13 HOLBOURNE STREET, UPPER KEDRON, QLD, 4055

STATUS
FOR APPROVAL

DRAWING TITLE
GROUND FLOOR - PLUMBING PLAN

REVIEWED
SR

APPROVED
LH

DRAWING NO.
A_1700

SCALE @ A3
1 : 100

PROJECT NO.
07-2025

REV NO.
G

SIGMA BUILDING CERTIFICATION

APPROVED


Subject to Compliance with conditions endorsed.

Building Certifier - C.L. Fung

QBCC No. A15040934

B.A. No.: 25017

Date: 17/12/2025

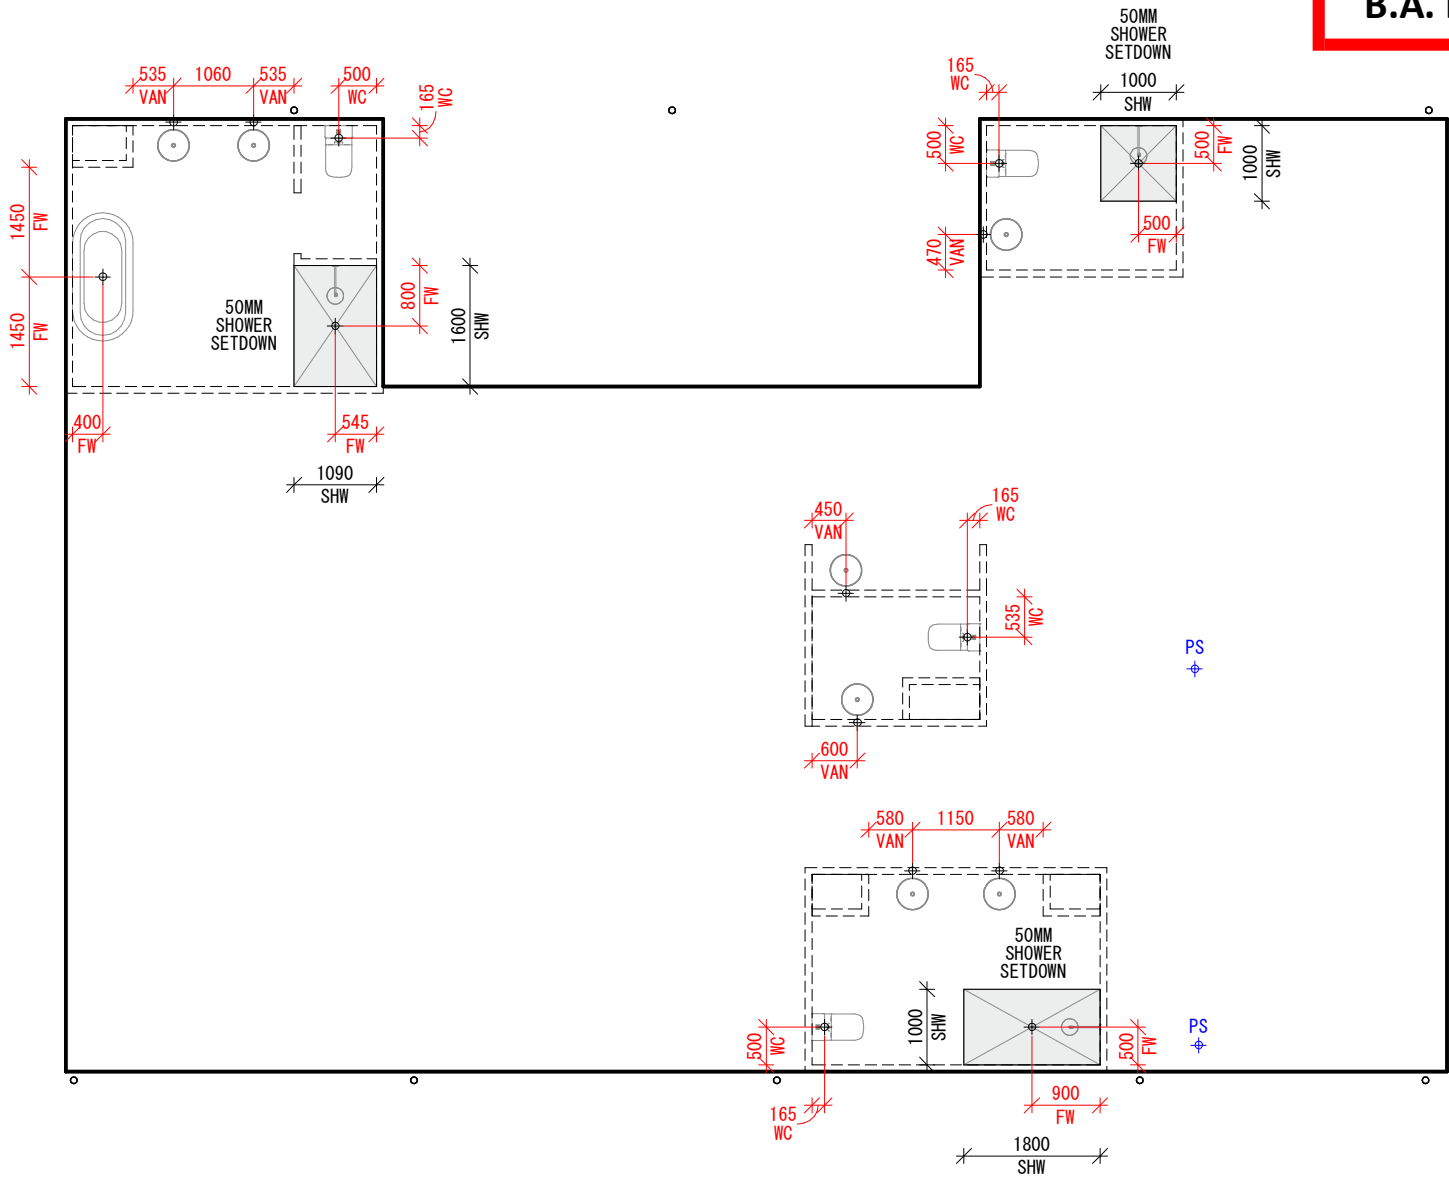

NOTE:
ALL PENETRATION DIMENSIONS ARE TAKEN FROM THE FRAME EDGE TO CL OF PENETRATION

PLUMBING LEGEND	
DP	DOWNPIPE
SHW	SHOWER
WC	TOILET
LT	LAUNDRY TUB
KS	KITCHEN SINK
FW	FLOOR WASTE
FWG	FLOOR WASTE GULLY
PS	PLUMBING STACK
VAN	VANITY
TAP	GARDEN TAP

REFERENCE

NORTH

NOTES

1. Do not scale drawing. Written dimensions govern
2. All dimensions are in millimeters unless noted otherwise
3. All dimensions shall be verified on site before proceeding with the work. The Architect shall be notified in writing of any discrepancies.
4. This drawing must be read in conjunction with all relevant contracts, specifications and drawings

REV DESCRIPTION

A	CONCEPT DESIGN
B	CONCEPT DESIGN
C	CONCEPT DESIGN
D	CONCEPT DESIGN
E	CONCEPT DESIGN
F	CONCEPT DESIGN
G	FOR APPROVAL

DATE

12.07.2025
19.07.2025
25.07.2025
02.08.2025
16.08.2025
01.09.2025
15.10.2025

CLIENT

PROJECT
LOT 5051, 13 HOLBOURNE STREET, UPPER KEDRON, QLD, 4055

STATUS

FOR APPROVAL

DRAWING TITLE

FIRST FLOOR - PLUMBING PLAN

REVIEWED

SR

APPROVED

LH

DRAWING NO.

A_1800

SCALE @ A3

1 : 100

PROJECT NO.

07-2025

REV NO.

G



ACN | 669 609 536
QBCC | 15405403



SIGMA BUILDING CERTIFICATION

APPROVED


Subject to Compliance with conditions endorsed.

Building Certifier - C.L. Fung

QBCC No. A15040934

B.A. No.: 25017

Date: 17/12/2025

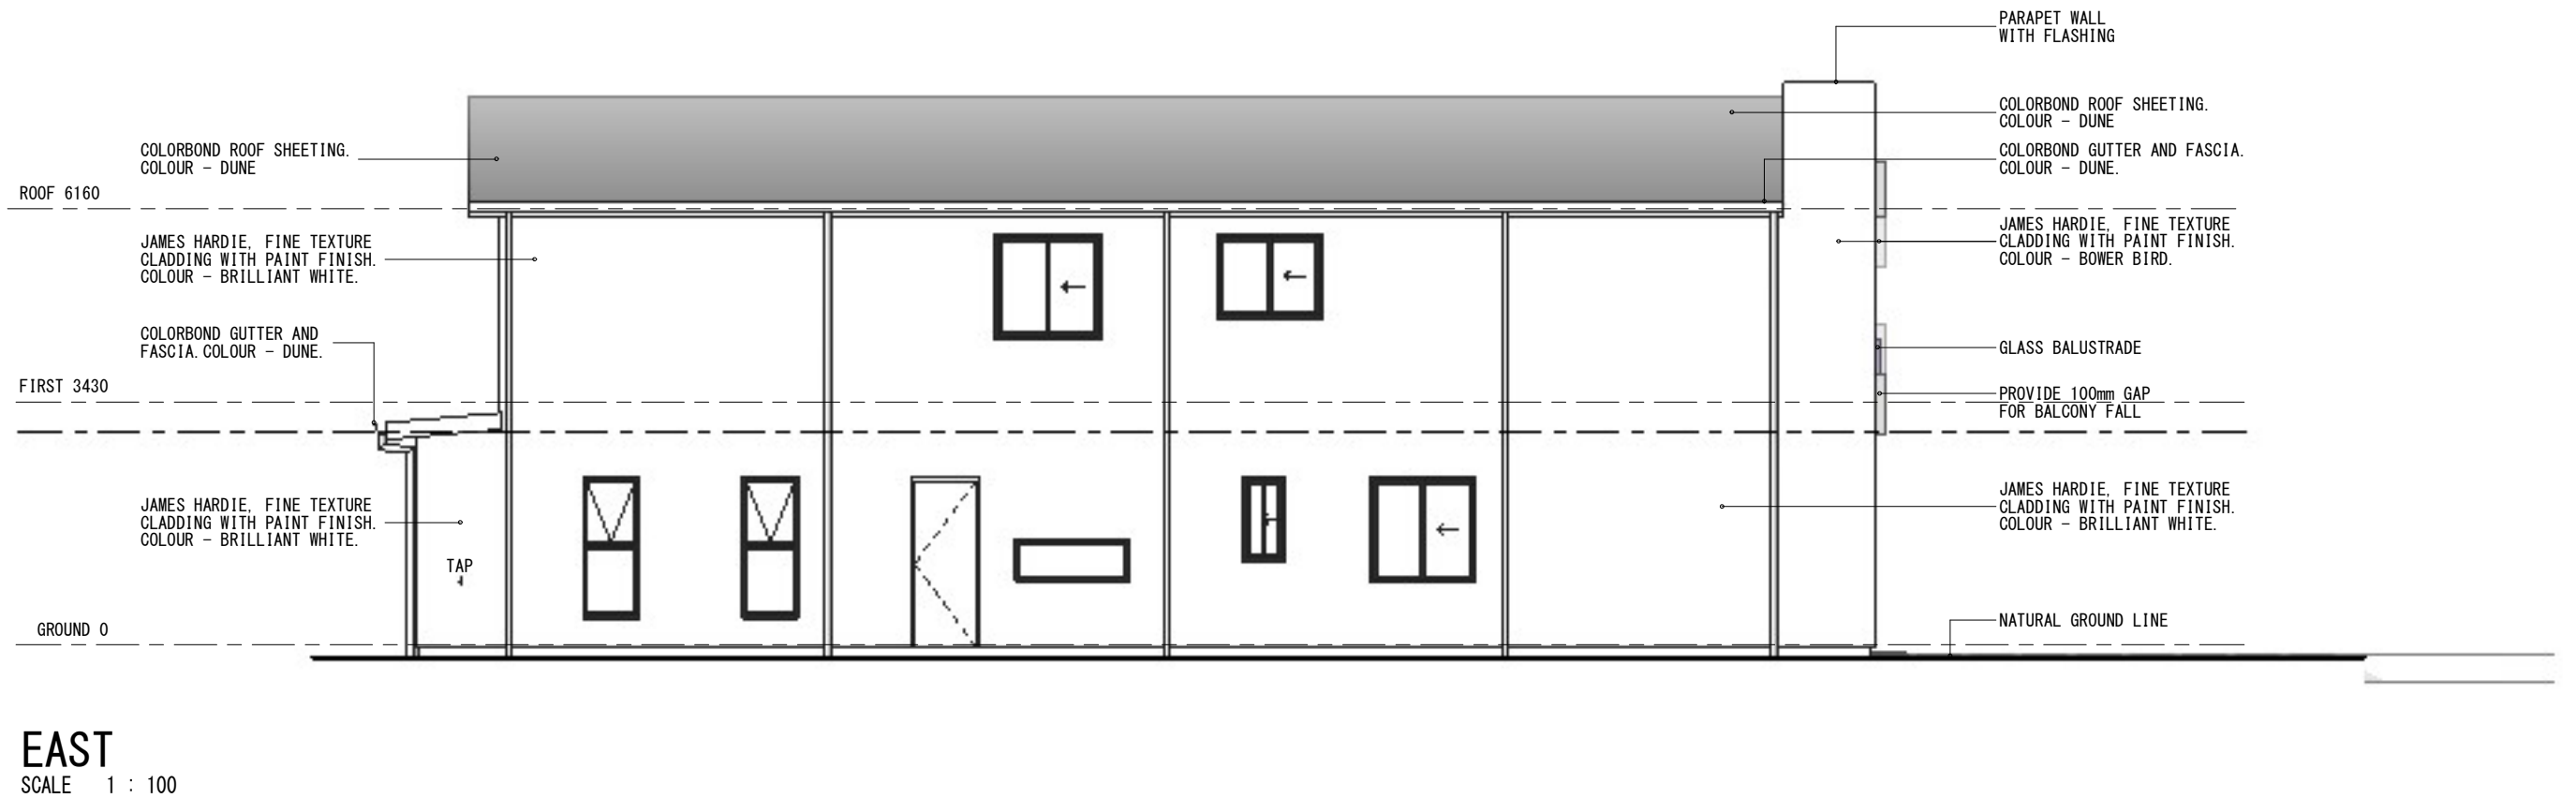



SOUTH
SCALE 1 : 100



WEST
SCALE 1 : 100

JAMES HARDIE, FINE TEXTURE
CLADDING WITH PAINT FINISH.
COLOUR - BRILLIANT WHITE.

COLORBOND ROOF SHEETING.
COLOUR - DUNE

COLORBOND GUTTER AND FASCIA.
COLOUR - DUNE.

JAMES HARDIE, FINE TEXTURE
CLADDING WITH PAINT FINISH.
COLOUR - BRILLIANT WHITE.

JAMES HARDIE, FINE TEXTURE
CLADDING WITH PAINT FINISH.
COLOUR - BRILLIANT WHITE.

NATURAL GROUND LINE

Subject to Compliance with conditions endorsed.

Building Certifier - C.L. Fung

QBCC No. A15040934

B.A. No.: 25017

Date: 17/12/2025

SIGMA BUILDING CERTIFICATION

APPROVED

COLORBOND ROOF SHEETING.
COLOUR - DUNE

COLORBOND GUTTER AND FASCIA.
COLOUR - DUNE.

JAMES HARDIE, FINE TEXTURE
CLADDING WITH PAINT FINISH.
COLOUR - BRILLIANT WHITE.

COLORBOND ROOF SHEETING.
COLOUR - DUNE

COLORBOND GUTTER AND FASCIA.
COLOUR - DUNE.

JAMES HARDIE, FINE TEXTURE
CLADDING WITH PAINT FINISH.
COLOUR - BRILLIANT WHITE.

NATURAL GROUND LINE

INSTANT HOT
WATER SYSTEM

AIR-CON
UNIT

MB

GMB

TAP

PARAPET WALL
WITH FLASHING

JAMES HARDIE, FINE TEXTURE
CLADDING WITH PAINT FINISH.
COLOUR - BOWER BIRD.

JAMES HARDIE, FINE TEXTURE
CLADDING WITH PAINT FINISH.
COLOUR - BRILLIANT WHITE.

WPC CLADDING.
COLOUR - MERBAU

JAMES HARDIE, FINE TEXTURE
CLADDING WITH PAINT FINISH.
COLOUR - BOWER BIRD.

JAMES HARDIE, FINE TEXTURE
CLADDING WITH PAINT FINISH.
COLOUR - PEBBLE BAY.

JAMES HARDIE, FINE TEXTURE
CLADDING WITH PAINT FINISH.
COLOUR - BRILLIANT WHITE.

REFERENCE

NORTH

NOTES

1. Do not scale drawing. Written dimensions govern
2. All dimensions are in millimeters unless noted otherwise
3. All dimensions shall be verified on site before proceeding with the work. The Architect shall be notified in writing of any discrepancies.
4. This drawing must be read in conjunction with all relevant contracts, specifications and drawings

REV DESCRIPTION

- | | |
|---|----------------|
| A | CONCEPT DESIGN |
| B | CONCEPT DESIGN |
| C | CONCEPT DESIGN |
| D | CONCEPT DESIGN |
| E | CONCEPT DESIGN |
| F | CONCEPT DESIGN |
| G | FOR APPROVAL |

DATE

- | |
|------------|
| 12.07.2025 |
| 19.07.2025 |
| 25.07.2025 |
| 02.08.2025 |
| 16.08.2025 |
| 01.09.2025 |
| 15.10.2025 |

CLIENT

PROJECT
LOT 5051, 13 HOLBOURNE
STREET, UPPER KEDRON, QLD, 4055

STATUS
FOR APPROVAL

DRAWING TITLE
EXTERNAL ELEVATIONS

REVIEWED
SR


APPROVED
LH

DRAWING NO.
A_2100

SCALE @ A3
1 : 100

PROJECT NO.
07-2025


REV NO.
G

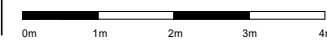

ACN 669 609 536
QBCC 15405403

LUXURIA HOMES

Experience The Epitome Of Luxury

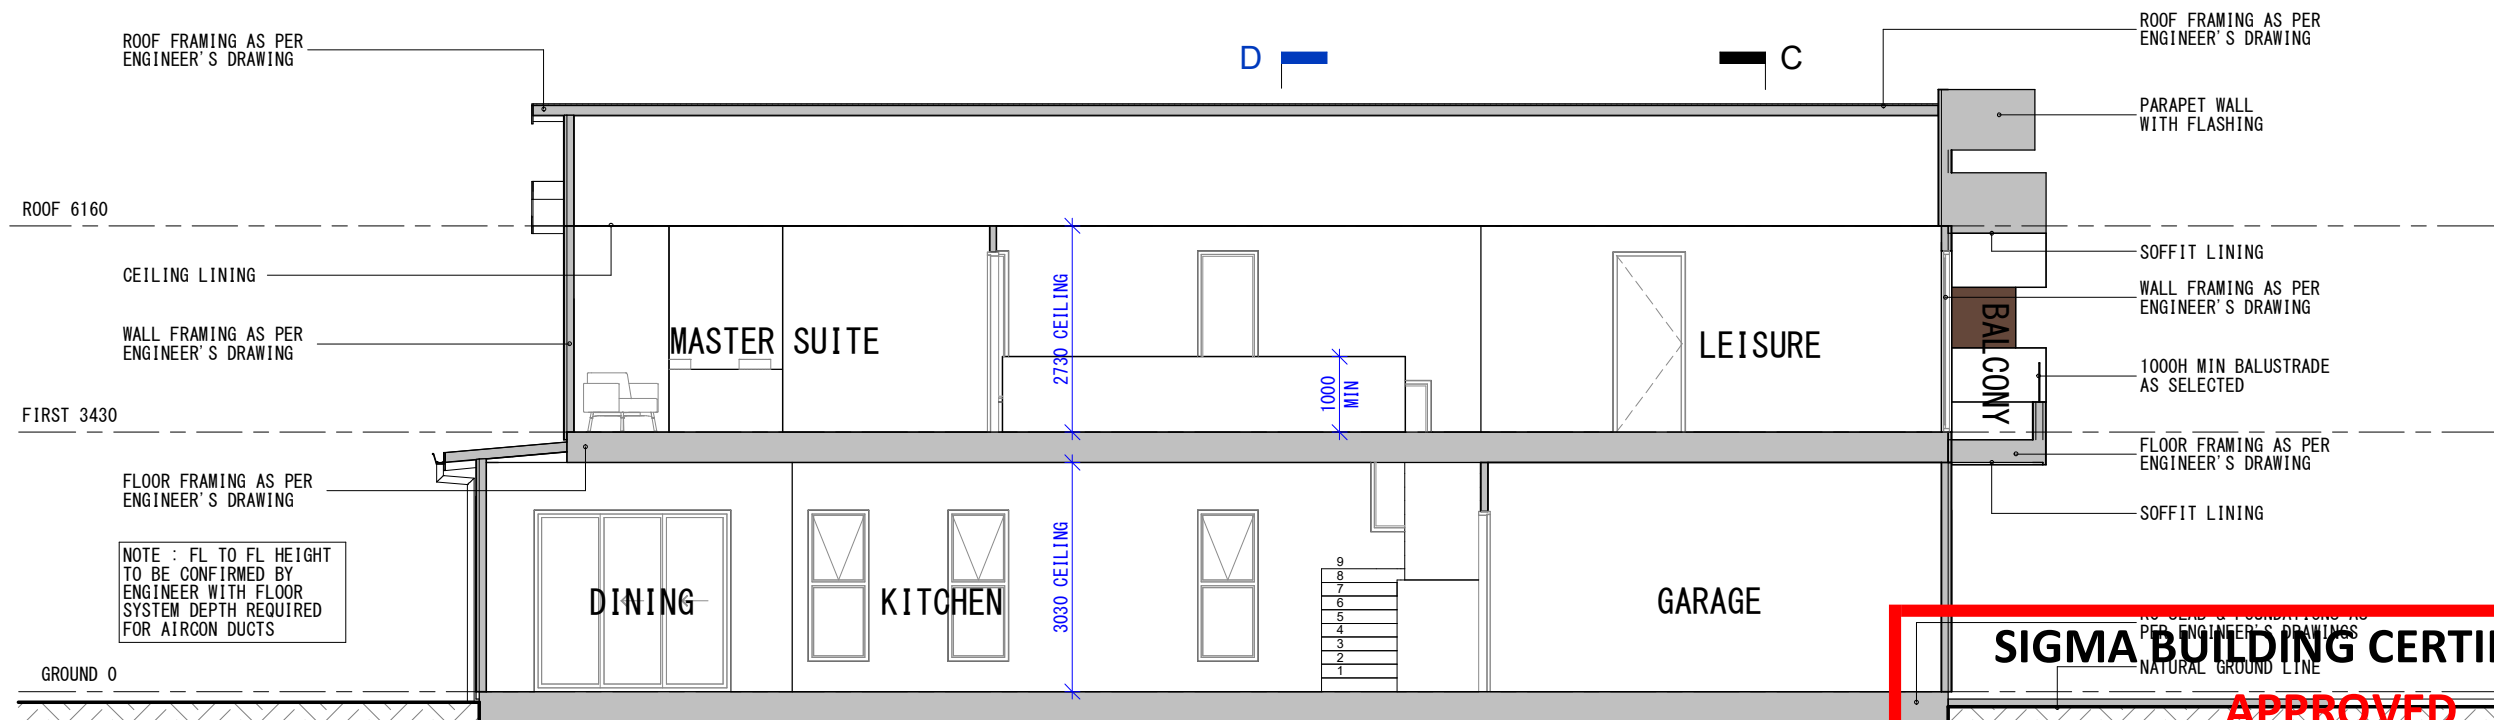

SIGMA BUILDING CERTIFICATION


APPROVED

Subject to Compliance with conditions endorsed.

Building Certifier - C.L. Fung
SECTION A-A
SCALE 1 : 100 QBCC No. A15040934


B.A. No.: 25017

Date: 17/12/2025

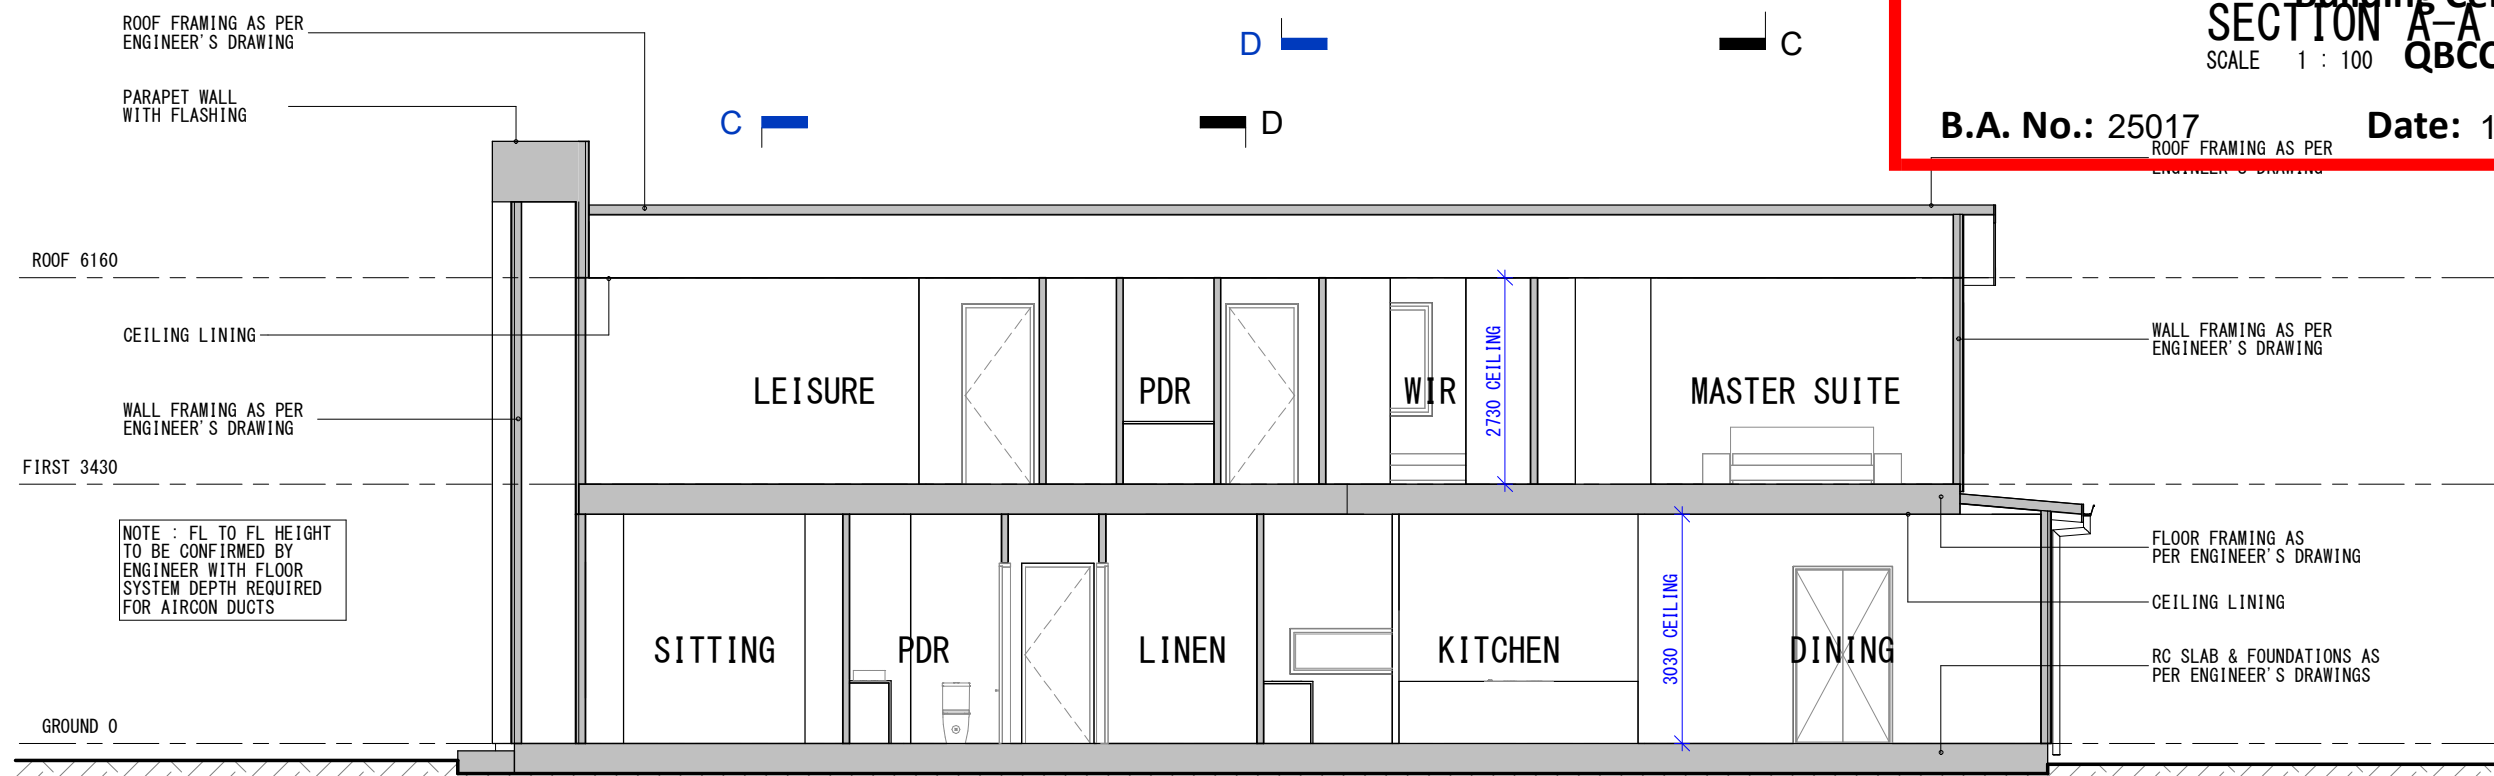

SECTION B-B

SCALE 1 : 100

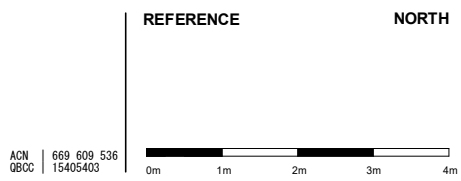

- NOTES**
1. Do not scale drawing. Written dimensions govern
 2. All dimensions are in millimeters unless noted otherwise
 3. All dimensions shall be verified on site before proceeding with the work. The Architect shall be notified in writing of any discrepancies.
 4. This drawing must be read in conjunction with all relevant contracts, specifications and drawings

REV	DESCRIPTION
A	CONCEPT DESIGN
B	CONCEPT DESIGN
C	CONCEPT DESIGN
D	CONCEPT DESIGN
E	CONCEPT DESIGN
F	CONCEPT DESIGN
G	FOR APPROVAL

DATE
12.07.2025
19.07.2025
25.07.2025
02.08.2025
16.08.2025
01.09.2025
15.10.2025

CLIENT

PROJECT
LOT 5051, 13 HOLBOURNE STREET, UPPER KEDRON, QLD, 4055

STATUS
FOR APPROVAL

DRAWING TITLE
SECTIONS

REVIEWED
SR


APPROVED
LH

DRAWING NO.
A_3000

SCALE @ A3
1 : 100

PROJECT NO.
07-2025

REV NO.
G

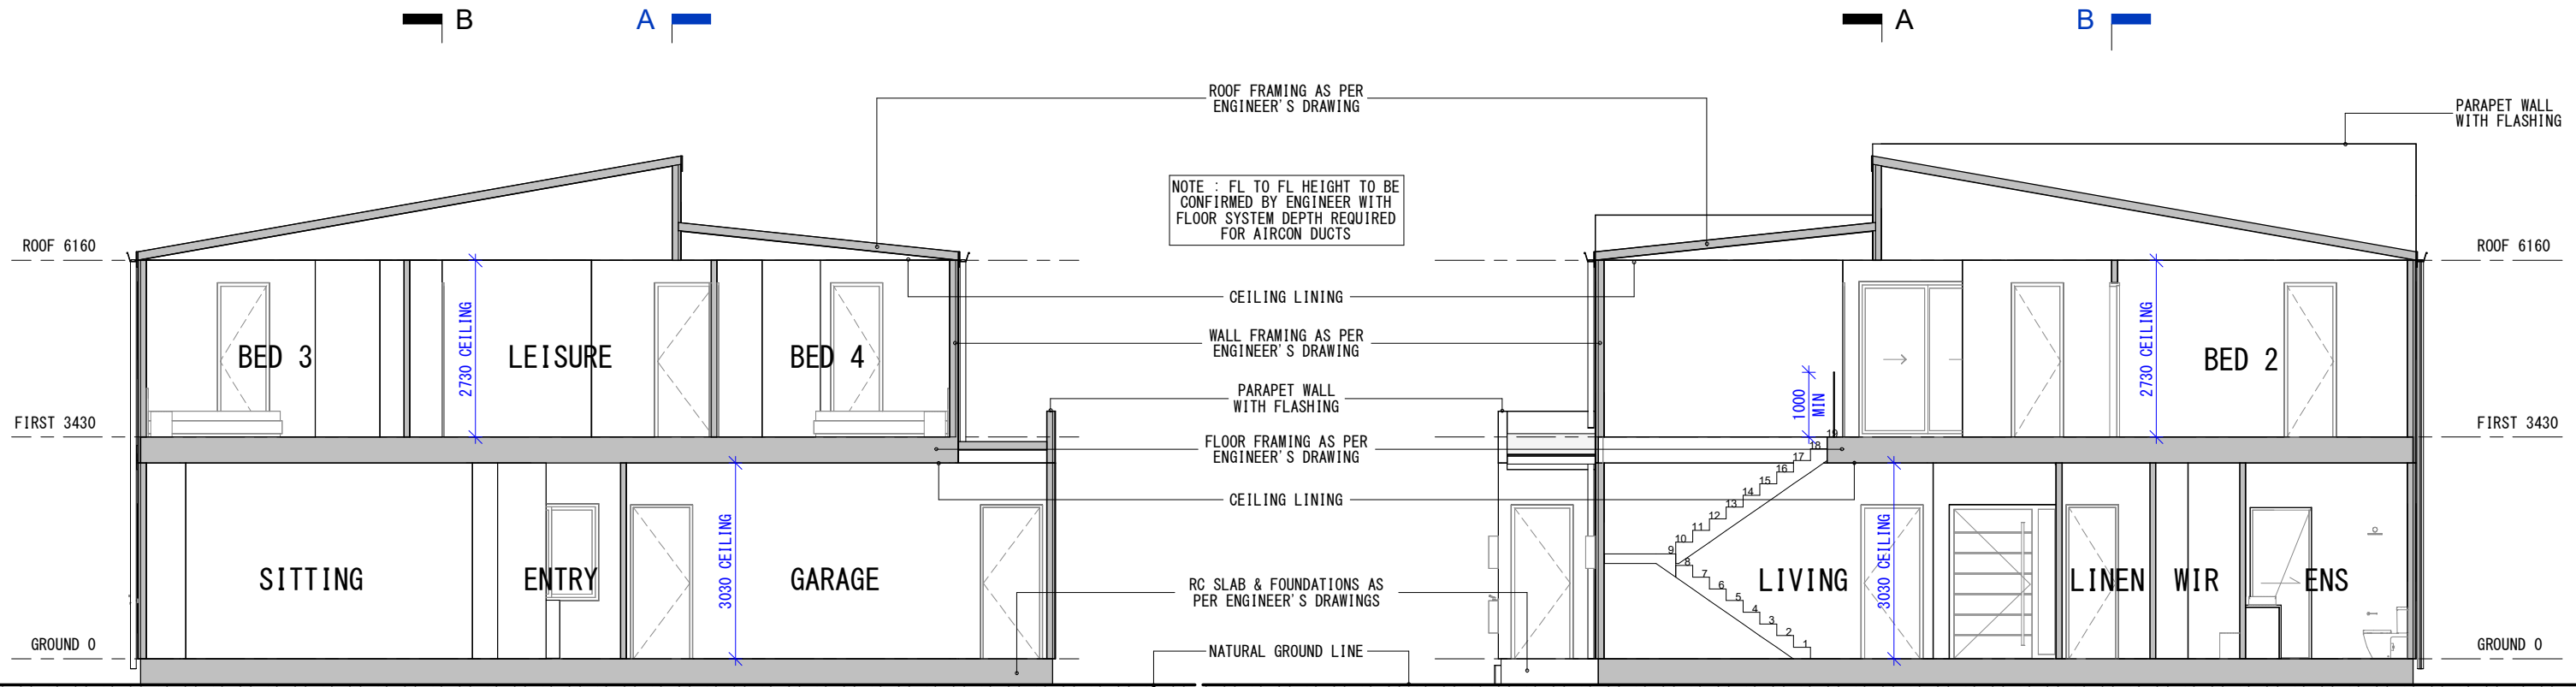

SECTION C-C
SCALE 1 : 100

SECTION D-D
SCALE 1 : 100

SIGMA BUILDING CERTIFICATION

APPROVED

Subject to Compliance with conditions endorsed.

Building Certifier - C.L. Fung

QBCC No. A15040934

B.A. No.: 25017

Date: 17/12/2025



ACN 669 609 536
QBCC 15405403

REFERENCE

NORTH

NOTES

1. Do not scale drawing. Written dimensions govern
2. All dimensions are in millimeters unless noted otherwise
3. All dimensions shall be verified on site before proceeding with the work. The Architect shall be notified in writing of any discrepancies.
4. This drawing must be read in conjunction with all relevant contracts, specifications and drawings

REV DESCRIPTION

- | | |
|---|----------------|
| A | CONCEPT DESIGN |
| B | CONCEPT DESIGN |
| C | CONCEPT DESIGN |
| D | CONCEPT DESIGN |
| E | CONCEPT DESIGN |
| F | CONCEPT DESIGN |
| G | FOR APPROVAL |

DATE

- | |
|------------|
| 12.07.2025 |
| 19.07.2025 |
| 25.07.2025 |
| 02.08.2025 |
| 16.08.2025 |
| 01.09.2025 |
| 15.10.2025 |

CLIENT

PROJECT
LOT 5051, 13 HOLBOURNE
STREET, UPPER KEDRON, QLD, 4055

STATUS
FOR APPROVAL

DRAWING TITLE
SECTIONS

REVIEWED
SR

APPROVED
LH

DRAWING NO.
A_3001

SCALE @ A3
1 : 100

PROJECT NO.
07-2025

REV NO.
G

DOORS

GROUND FLOOR

ID No.	D01	D02	D03	ID. 01, ID. 02	ID. 03, ID. 05, ID. 07	ID. 04	ID. 06
LOCATION	ENTRY	LAUNDRY	GARAGE	LINEN, PDR	BED 5, L' DRY, GARAGE	BED 5 ENS	MEDIA
LEAF HEIGHT	2400	2340	2340	2340	2340	2340	2340
LEAF WIDTH	1200	870	870	720	870	870	2/620
ELEVATION							
DOOR TYPE	AS SELECTED	GLASS AS SELECTED	AS SELECTED	HINGED DOOR	HINGED DOOR	CAVITY SLIDER	AS SELECTED
QUANTITY	1	1	1	2	3	1	1

GROUND FLOOR

ID No.	D04
LOCATION	GARAGE
LEAF HEIGHT	2400
LEAF WIDTH	4800
ELEVATION	
DOOR TYPE	SECTIONAL DOOR AS SELECTED
QUANTITY	1

FIRST FLOOR

ID. 08, ID. 10, ID. 12, ID. 16	ID. 09, ID. 11, ID. 13, ID. 14, ID. 15, ID. 17
BED 4, BED 3, BED 2, MASTER	ENS, SHARED BATH, WIL, PDR, WC
2340	2340
820	720
ELEVATION	
HINGED DOOR	HINGED DOOR
4	6

WINDOWS

GROUND FLOOR

ID No.	W01	W02, W07	W03	W04	W05, W06, W10, W11, W12	W08, W09	W13
LOCATION	SITTING	BED 5, DINING	ENS	PANTRY	MEDIA, LIVING	DINING, LIVING	STAIR
HEIGHT	1800	1500	1200	600	2000	2400	2000
WIDTH	1500	1500	600	1600	800	2600	800
ELEVATION							
WINDOW TYPE	SLIDER OX	SLIDER OX	SLIDER OX	FIXED	AWNING	STACKER DOOR - RECESSED	FIXED
QUANTITY	1	2	1	1	5	2	1

SIGMA BUILDING CERTIFICATION

APPROVED

Subject to Compliance with conditions endorsed.

Building Certifier - C.L. Fung

QBCC No. A15040934

B.A. No.: 25017

Date: 17/12/2025

WINDOWS

FIRST FLOOR

ID No.	W14	W15	W16	W17	W18	W19	W20	W21	W22	W23, W24	W25
LOCATION	BED 4	LEISURE	BED 3	SHARED BATH	BED 2	MASTER ENSUITE	MASTER SUITE	SHARED BATH	WC	LIVING VOID	BED 4 ENS
HEIGHT	2400	2400	1800	1200	1500	2000	1500	1200	1200	2000	1200
WIDTH	1800	3100	1500	1500	1500	800	1500	1500	600	800	900
ELEVATION											
WINDOW TYPE	SLIDER DOOR	SLIDER OX	SLIDER OX	SLIDER OX - OBSCURED	SLIDER OX - OBSCURED	AWNING - OBSCURED	SLIDER OX	SLIDER OX	SLIDER OX	FIXED	SLIDER OX
QUANTITY	1	1	1	1	1	1	1	1	1	2	1

NOTE:

ALL WINDOW SIZES ARE INDICATIVE ONLY. REFER TO MANUFACTURERS SPECIFICATION FOR WINDOW & DOOR SIZES AND OPENINGS

ALL REVEAL SIZES TO SUIT WALL THICKNESS. REFER TO FLOOR PLANS FOR DETAILS.

REFER TO ENERGY EFFICIENCY REPORT FOR GLAZING SPECIFICATIONS.

REFER TO PLANS FOR SLIDING DOORS & WINDOWS OPENING DIRECTIONS


PROVIDE FLY SCREENS TO ALL OPENING WINDOWS INCLUDING SLIDING GLASS DOORS



ACN 669 609 536
QBCC 15405403

REFERENCE

NORTH

 

NOTES

1. Do not scale drawing. Written dimensions govern
2. All dimensions are in millimeters unless noted otherwise
3. All dimensions shall be verified on site before proceeding with the work. The Architect shall be notified in writing of any discrepancies.
4. This drawing must be read in conjunction with all relevant contracts, specifications and drawings

REV DESCRIPTION

- | | |
|---|----------------|
| A | CONCEPT DESIGN |
| B | CONCEPT DESIGN |
| C | CONCEPT DESIGN |
| D | CONCEPT DESIGN |
| E | CONCEPT DESIGN |
| F | CONCEPT DESIGN |
| G | FOR APPROVAL |

DATE

- | |
|------------|
| 12.07.2025 |
| 19.07.2025 |
| 25.07.2025 |
| 02.08.2025 |
| 16.08.2025 |
| 01.09.2025 |
| 15.10.2025 |

CLIENT

PROJECT
LOT 5051, 13 HOLBOURNE
STREET, UPPER KEDRON, QLD, 4055

STATUS
FOR APPROVAL

DRAWING TITLE
WINDOW & DOOR SCHEDULE

REVIEWED
SR

APPROVED
LH

DRAWING NO.
A_5000

SCALE @ A3
1 : 100

PROJECT NO.
07-2025

REV NO.
G

SIGMA BUILDING CERTIFICATION

APPROVED


Subject to Compliance with conditions endorsed.

Building Certifier - C.L. Fung

QBCC No. A15040934

B.A. No.: 25017

Date: 17/12/2025

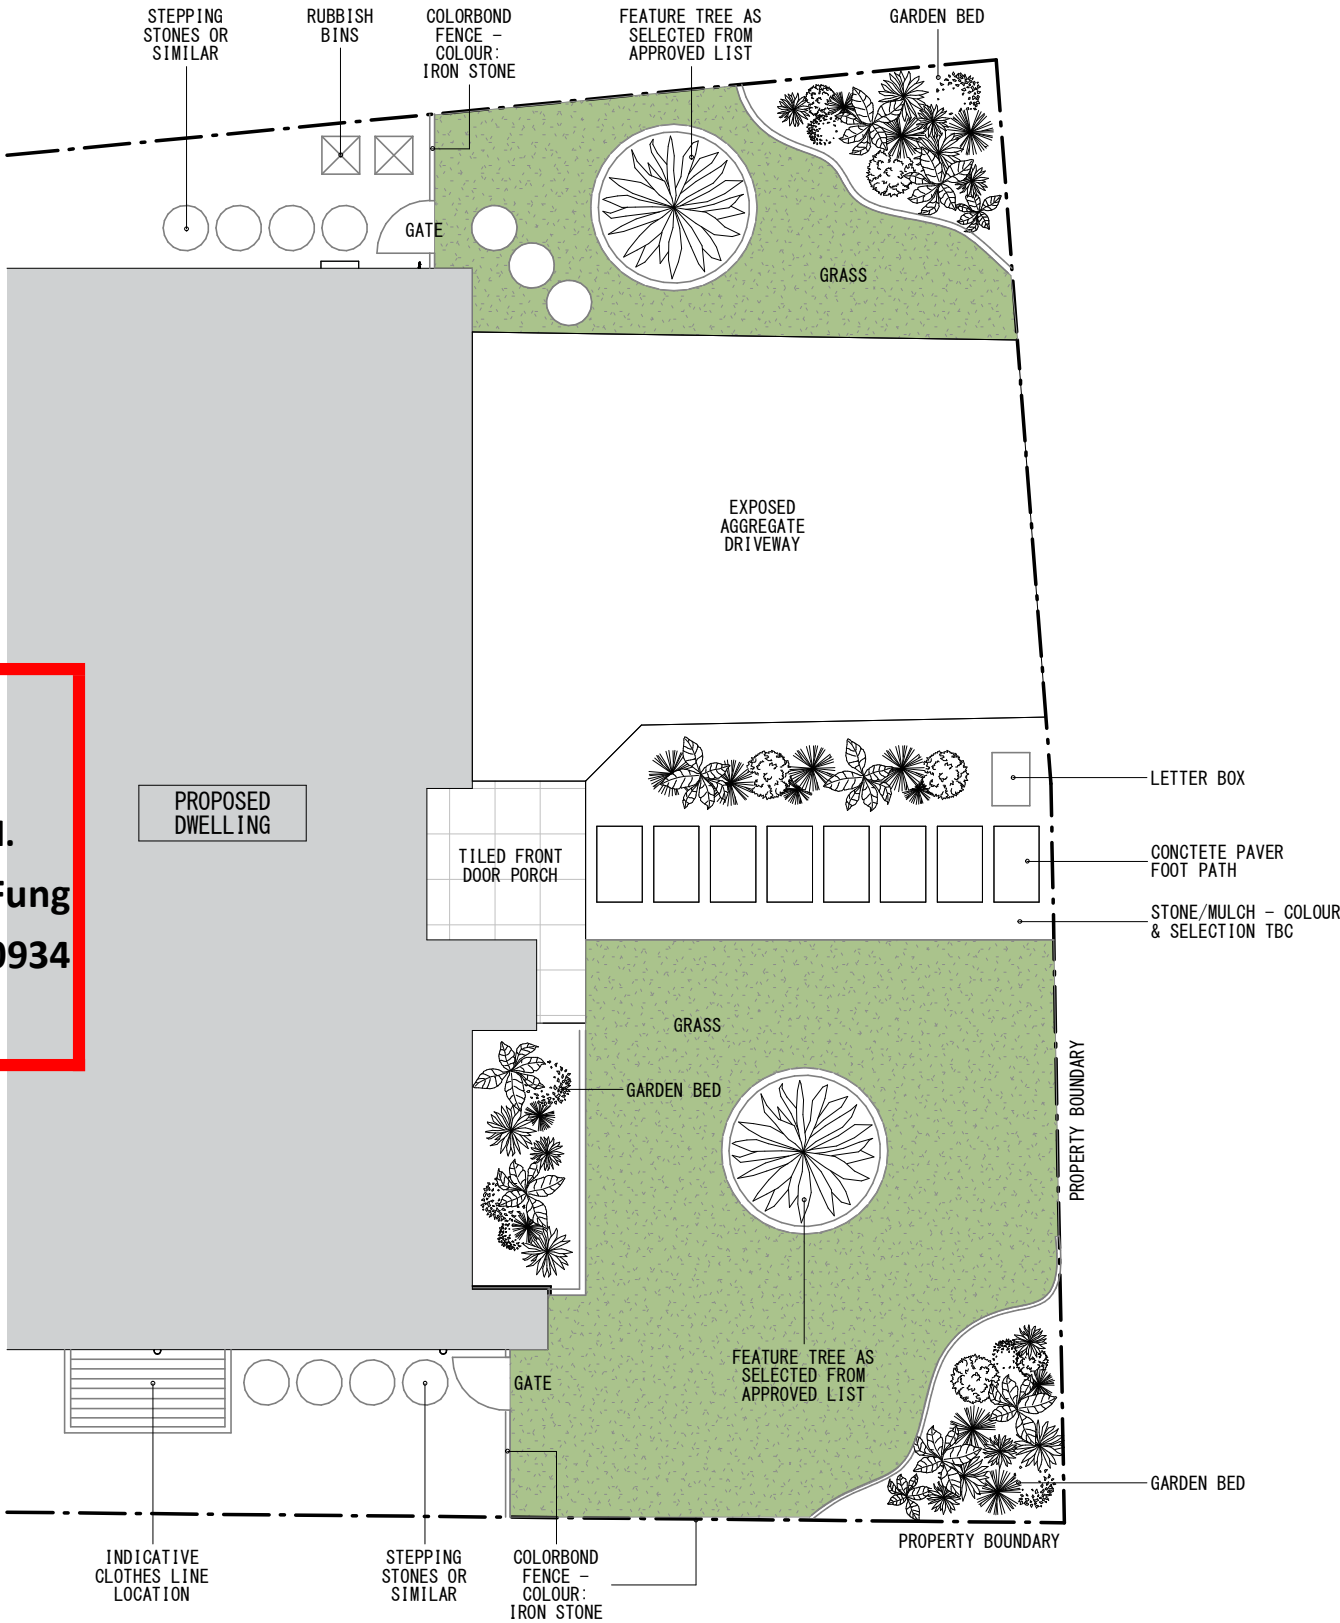


- PLANT SCHEDULE**
- FEATURE PLANT - QTY 12
 - SHRUB - QTY 10
 - SHRUB - QTY 10
 - GROUND COVER - QTY 15
 - GROUND COVER - QTY 15
 - TREES (LARGE VERSION) - QTY 1
- NOTE** - ALL PLANTS TO BE SELECTED FROM APPROVED LANDSCAPING/PLANTING LIST SUPPLIED BY DEVELOPER



ACN 669 609 536
QBCC 15405403

REFERENCE

 

NORTH

NOTES

1. Do not scale drawing. Written dimensions govern
2. All dimensions are in millimeters unless noted otherwise
3. All dimensions shall be verified on site before proceeding with the work. The Architect shall be notified in writing of any discrepancies.
4. This drawing must be read in conjunction with all relevant contracts, specifications and drawings

REV DESCRIPTION

- | | |
|---|----------------|
| A | CONCEPT DESIGN |
| B | CONCEPT DESIGN |
| C | CONCEPT DESIGN |
| D | CONCEPT DESIGN |
| E | CONCEPT DESIGN |
| F | CONCEPT DESIGN |
| G | FOR APPROVAL |

DATE

- | |
|------------|
| 12.07.2025 |
| 19.07.2025 |
| 25.07.2025 |
| 02.08.2025 |
| 16.08.2025 |
| 01.09.2025 |
| 15.10.2025 |

CLIENT

PROJECT
LOT 5051, 13 HOLBOURNE STREET, UPPER KEDRON, QLD, 4055

STATUS
FOR APPROVAL

DRAWING TITLE
LANDSCAPE DESIGN

REVIEWED
TR

APPROVED
SR

DRAWING NO.
A_6000

SCALE @ A3
As indicated

PROJECT NO.
07-2025

REV NO.
G